



Project: 26-29

Project Location: Pasig City

1) D-1: Frameless Glass Door

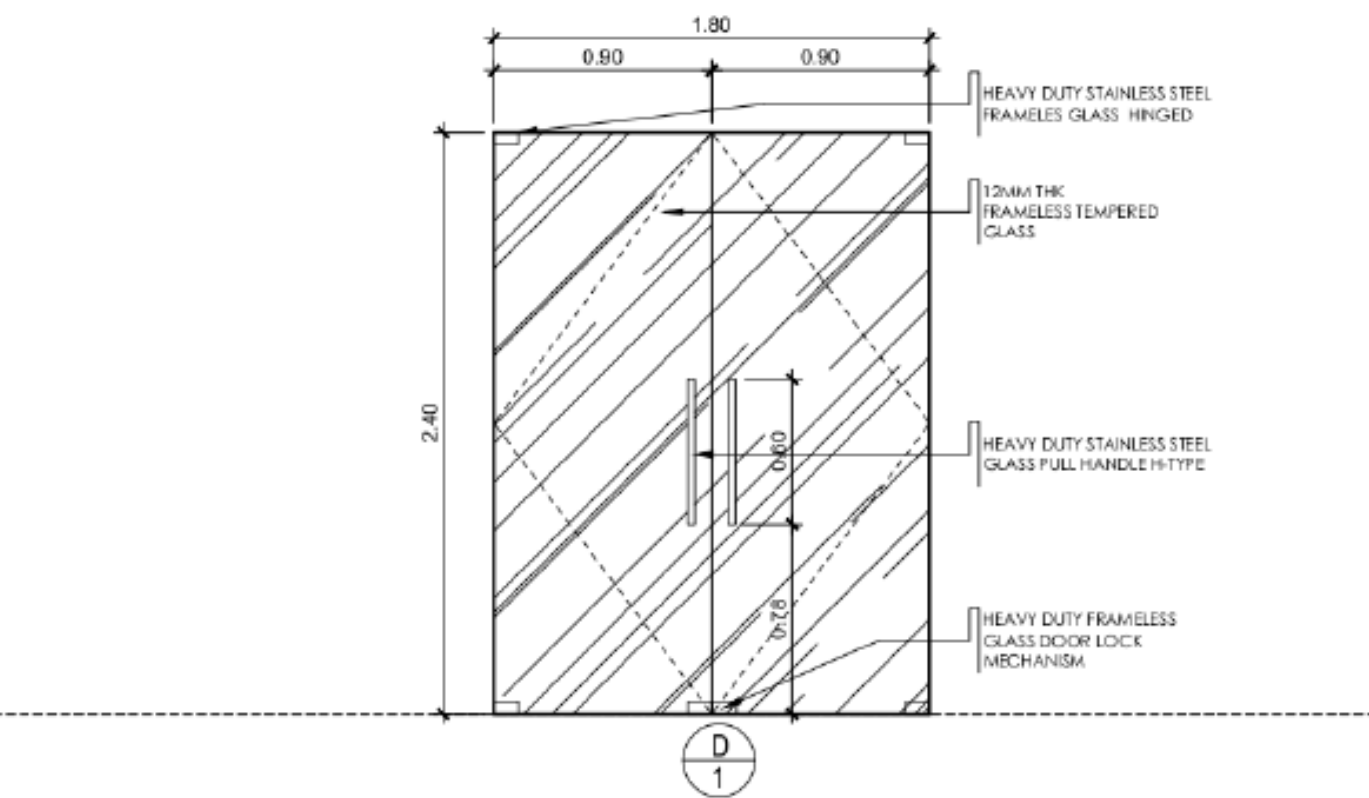


TYPE:	DOUBLE LEAF DOUBLE ACTION SWING GLASS DOOR
DESCRIPTION:	12MM THK TEMPERED GLASS FRAMELESS DOOR W/ HEAVY DUTY DOOR LOCK AND H-TYPE STAINLESS STEEL PULL HANDLE
LOCATION:	ENTRANCE 1 & 2
REQUIREMENTS:	2 SET

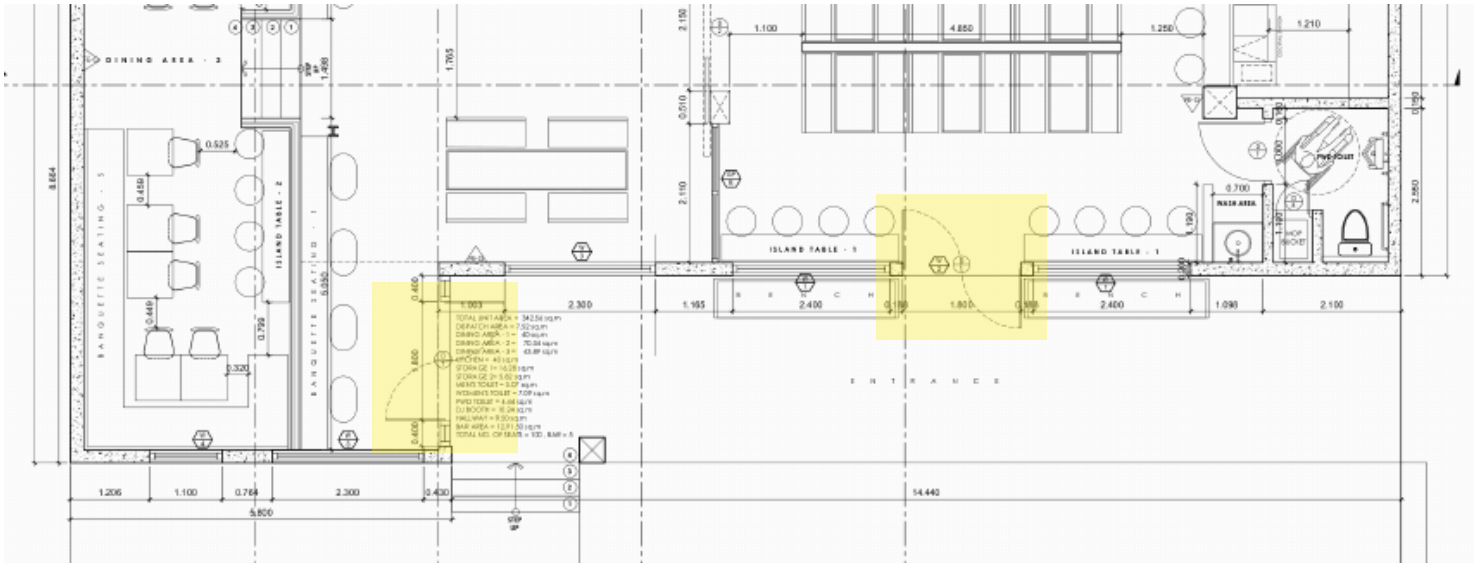



Project: 26-29

Project Location: Pasig City

2) D-2: Sliding Framed Glass Door

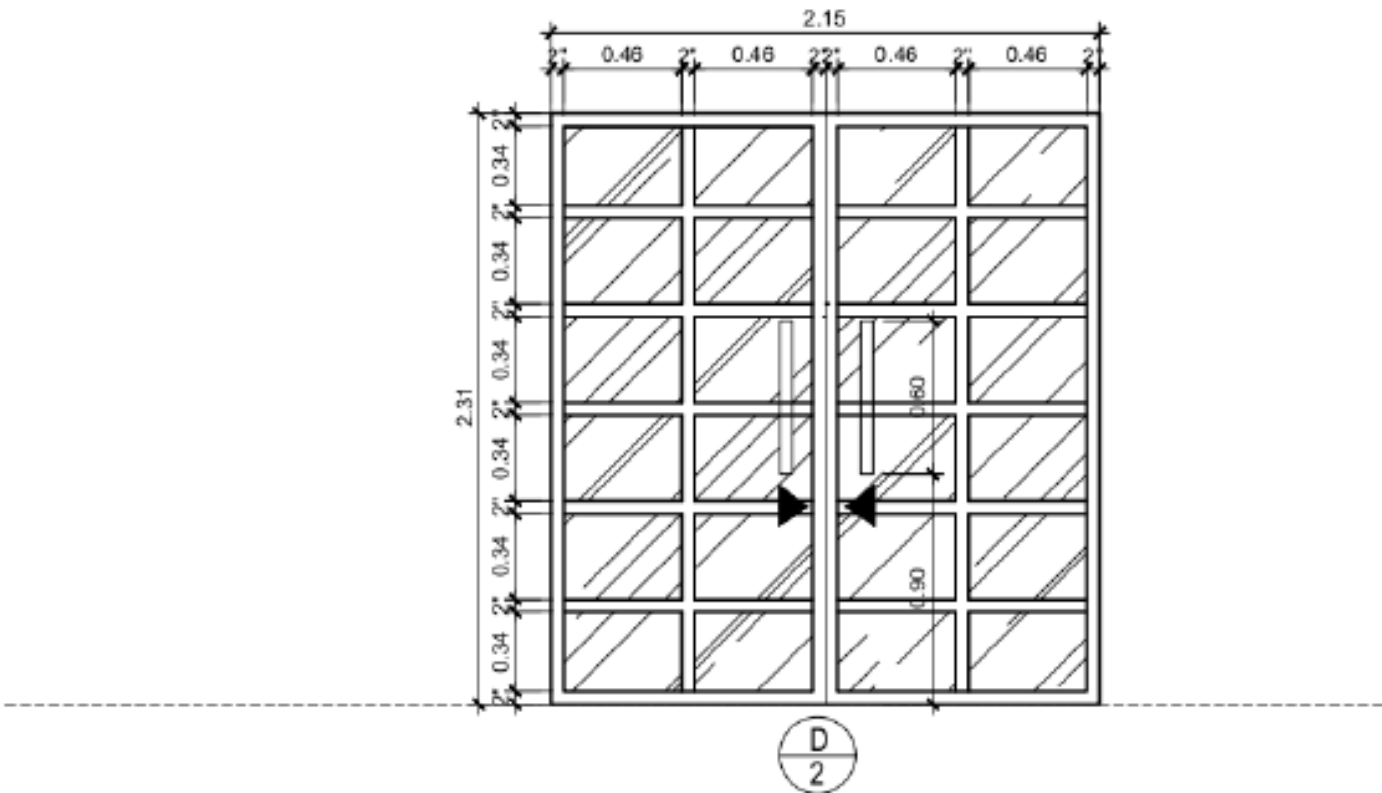


TYPE:	SLIDING DOOR
DESCRIPTION:	12MM THK TEMPERED GLASS W/ 2" x 2" ALUMINUM FRAMING WITH H-TYPE STAINLESS STEEL PULL HANDLE
LOCATION:	DINING AREA - 1
REQUIREMENTS:	1 SET

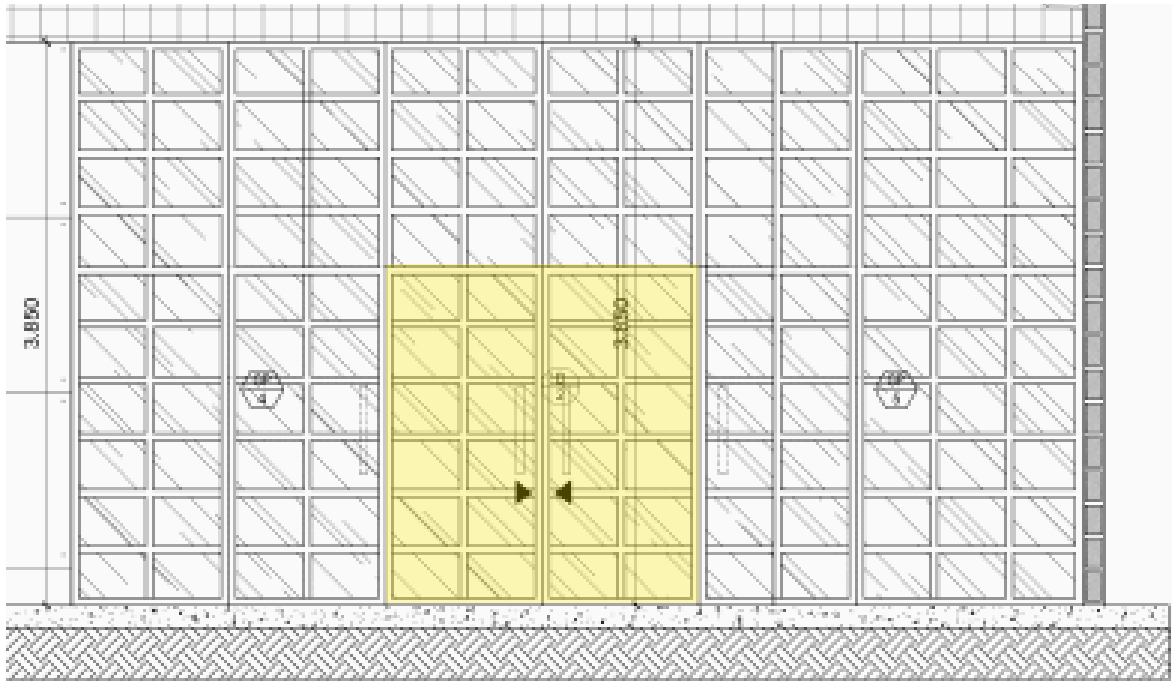
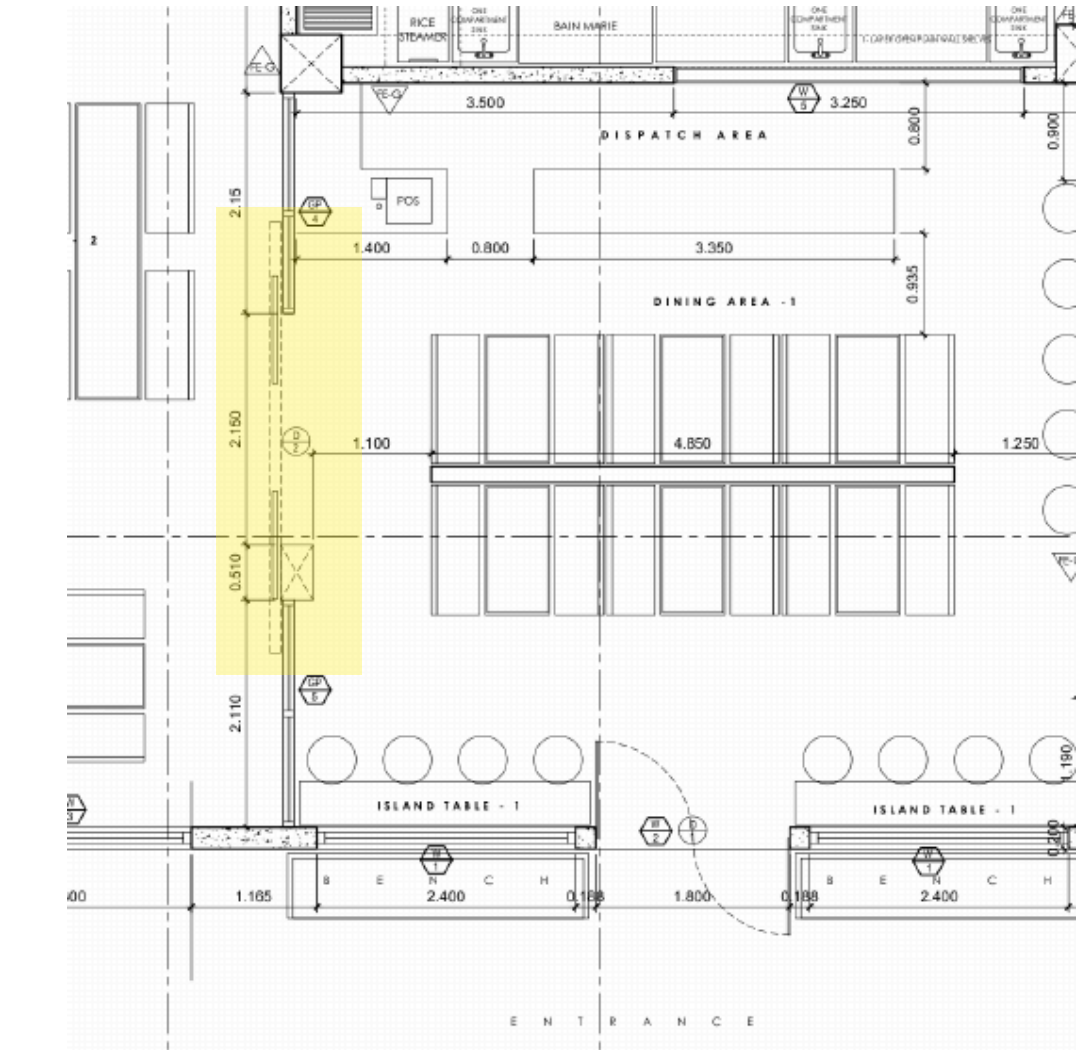


Project: 26-29
Project Location: Pasig City

3) D-5: Swing Framed Glass Door

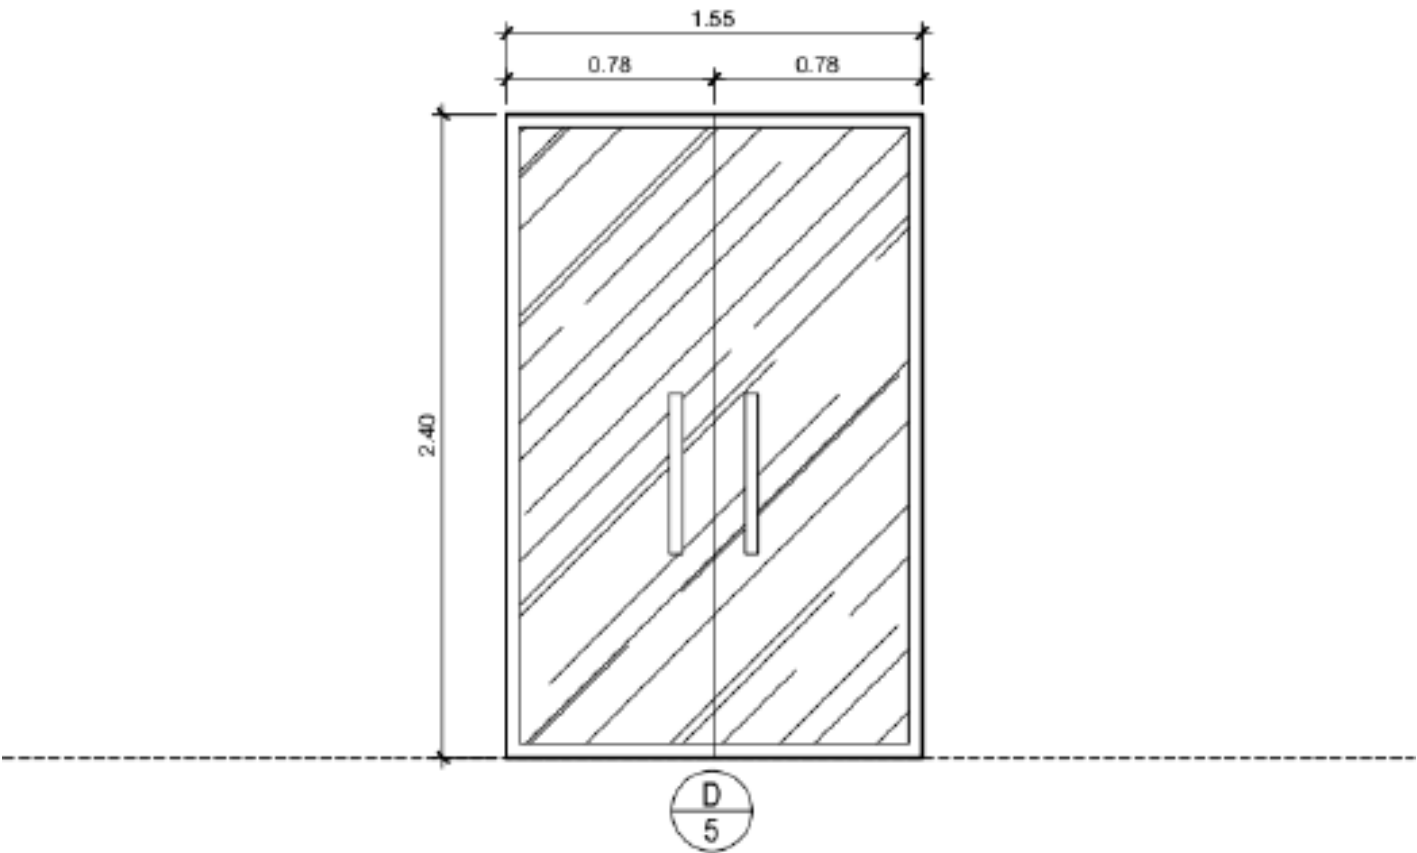


TYPE:	DOUBLE LEAF SWING DOOR
DESCRIPTION:	12MM THK TEMPERED GLASS W/ 2" x 2' ALUMINUM FRAMING WITH H-TYPE STAINLESS STEEL PULL HANDLE
LOCATION:	SMOKING AREA
REQUIREMENTS:	1 SET

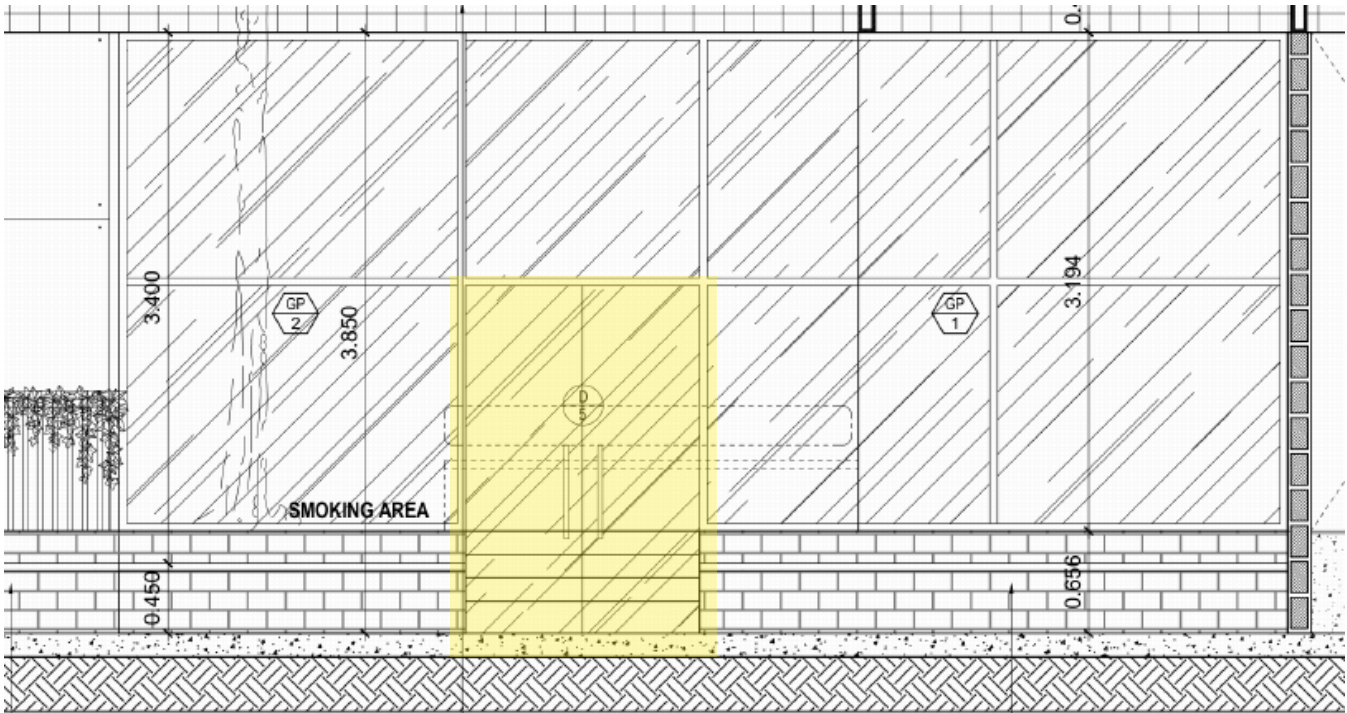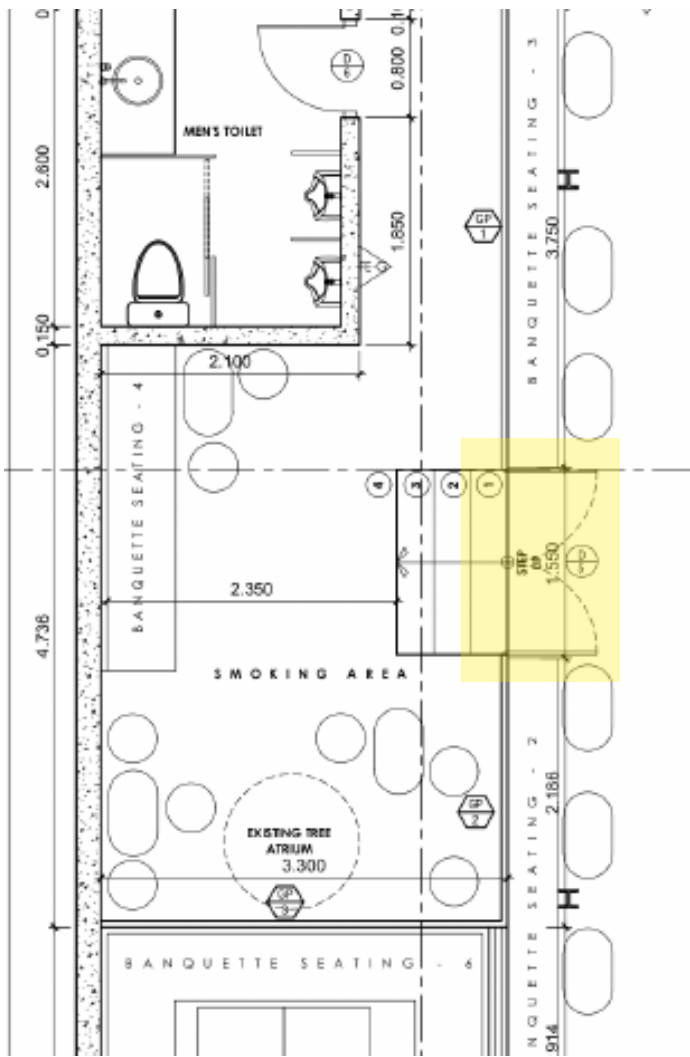



Project: 26-29

Project Location: Pasig City

4) W-1: Fixed Window

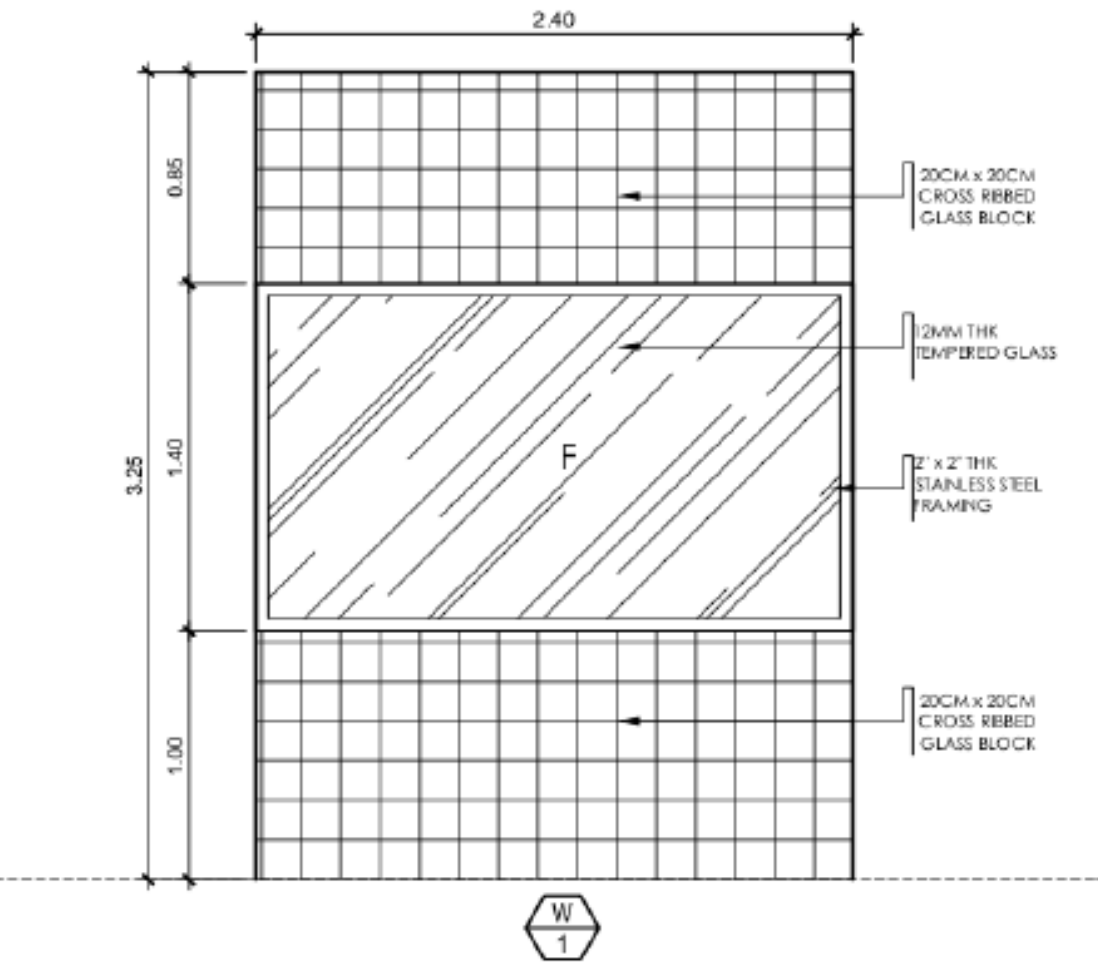


TYPE:	FIXED WINDOW
DESCRIPTION:	20CM x 20CM CROSS RIBBED GLASS BLOCK , 12MM THK TEMPERED GLASS WITH 2" x 2" THK STAINLESS STEEL FRAMING
LOCATION:	ENTRANCE AREA
REQUIREMENTS:	2 SET

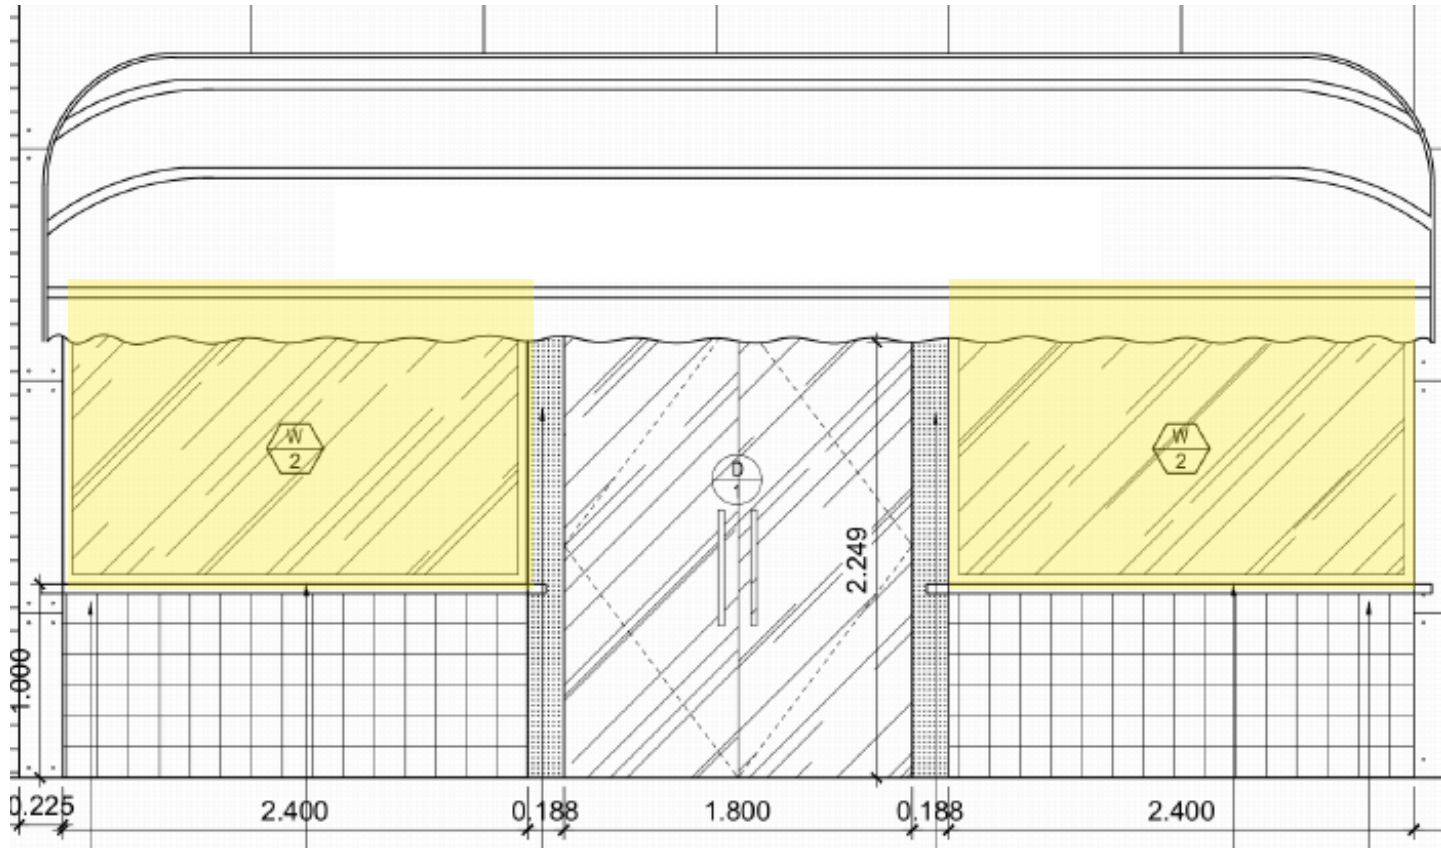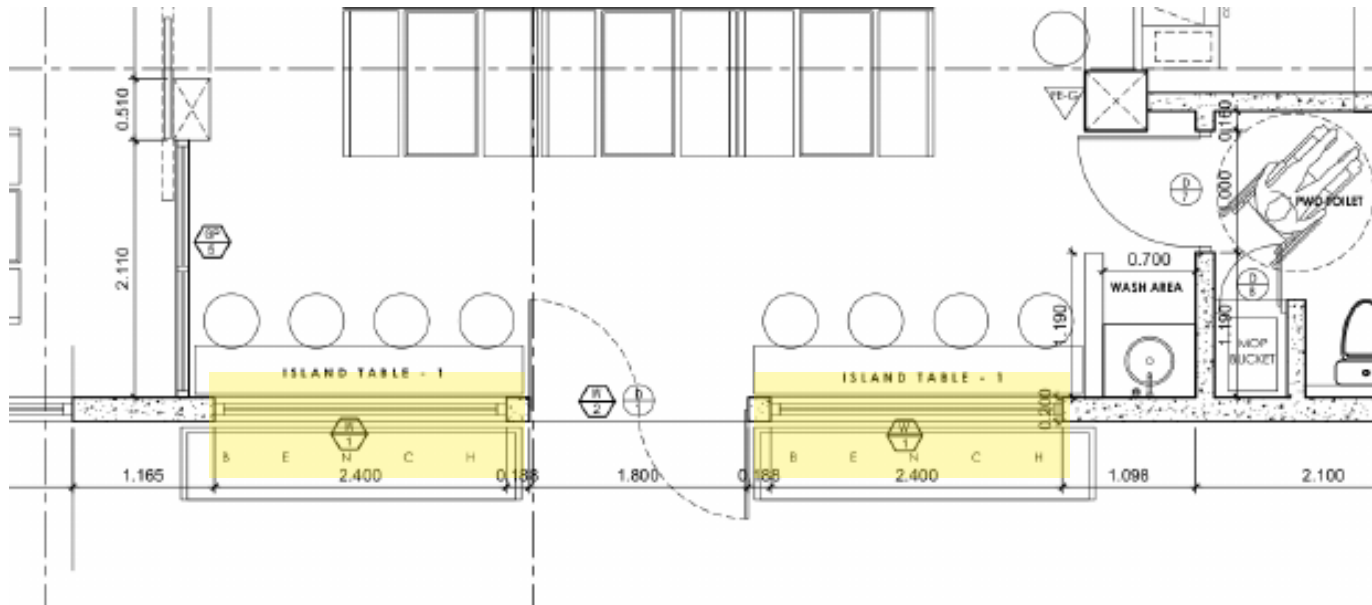



Project: 26-29

Project Location: Pasig City

5) W-3: Big Fixed Round Glass

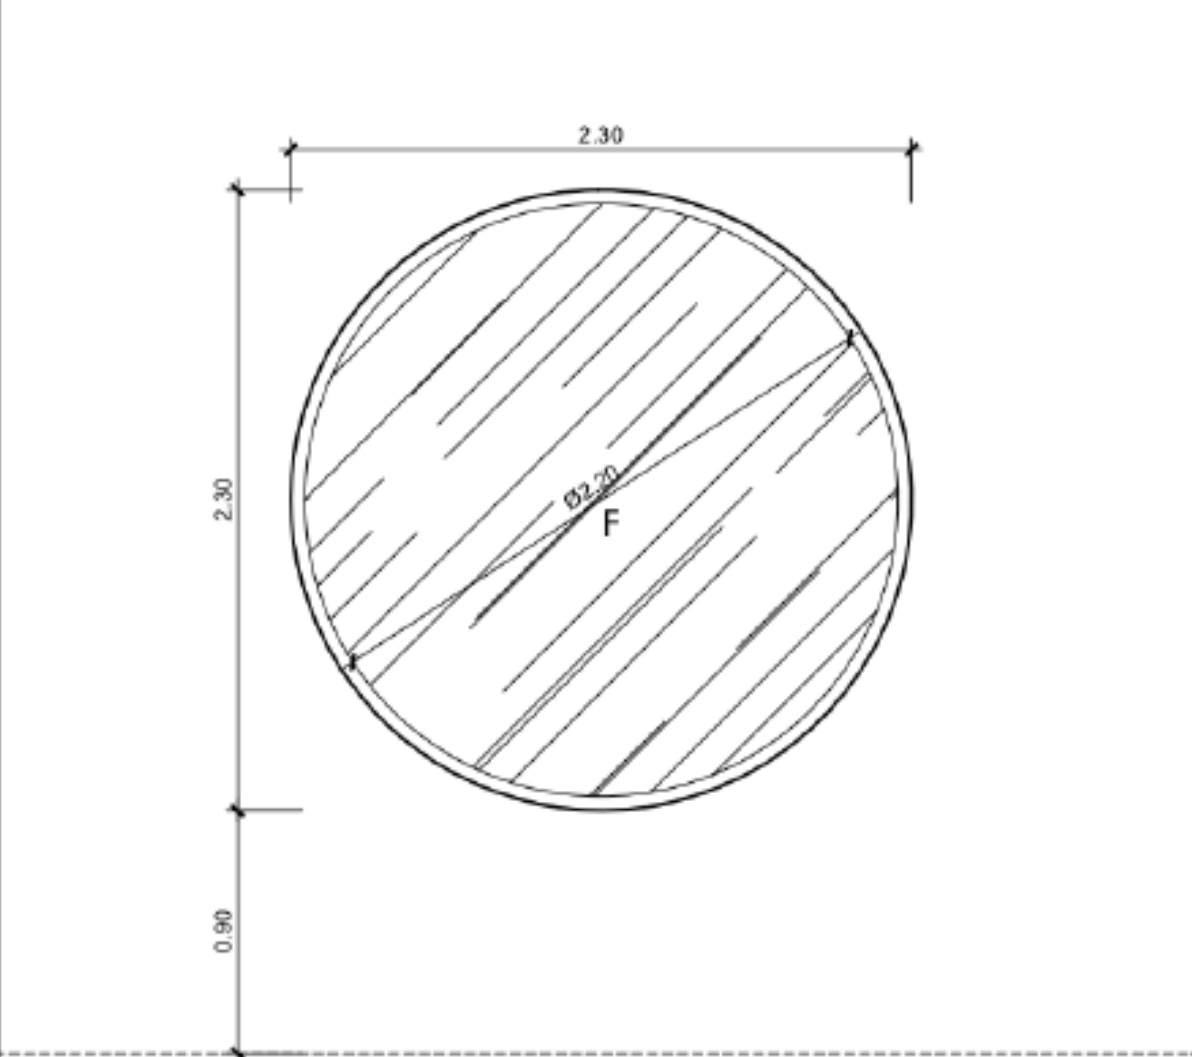


TYPE:	FIXED WINDOW
DESCRIPTION:	12MM THK TEMPERED GLASS WITH 2" x 2" BLACK ANONIZED ALUMINUM FRAMING
LOCATION:	ENTRANCE AREA
REQUIREMENTS:	2 SET

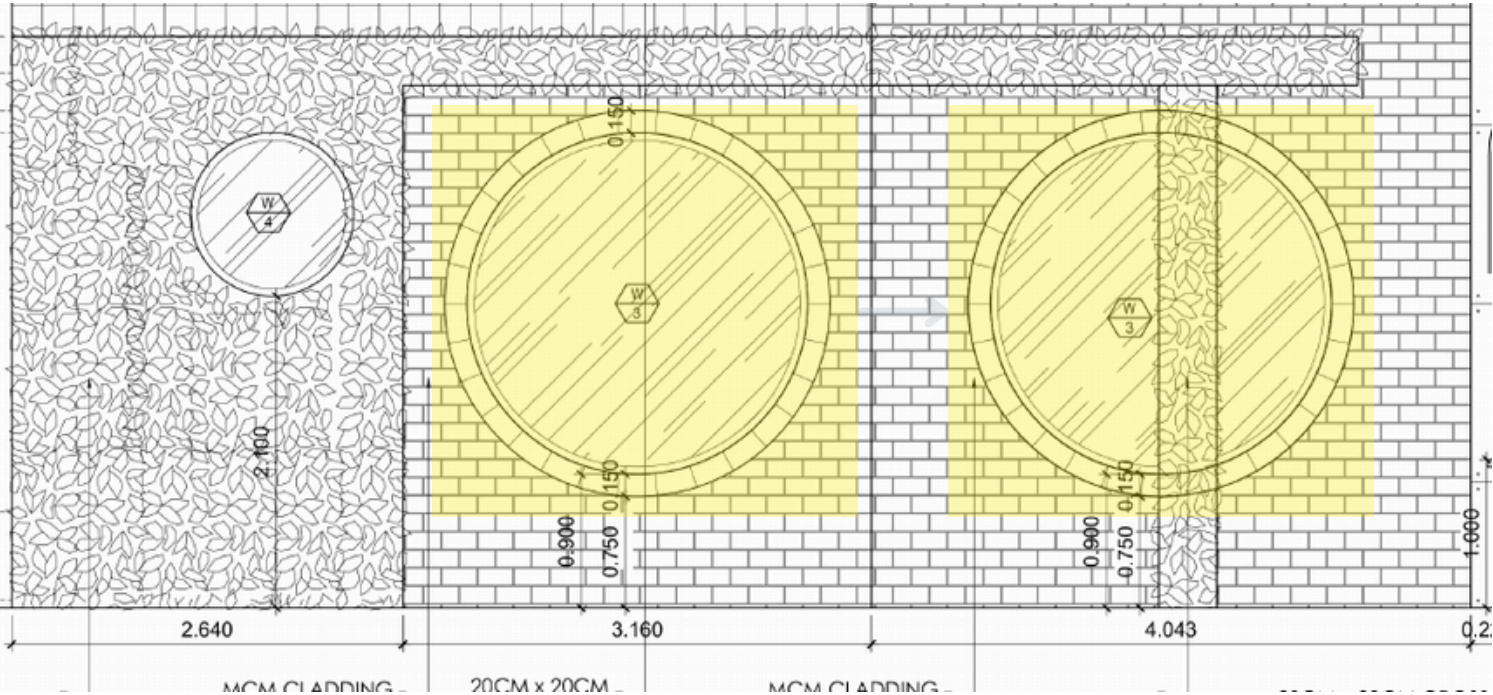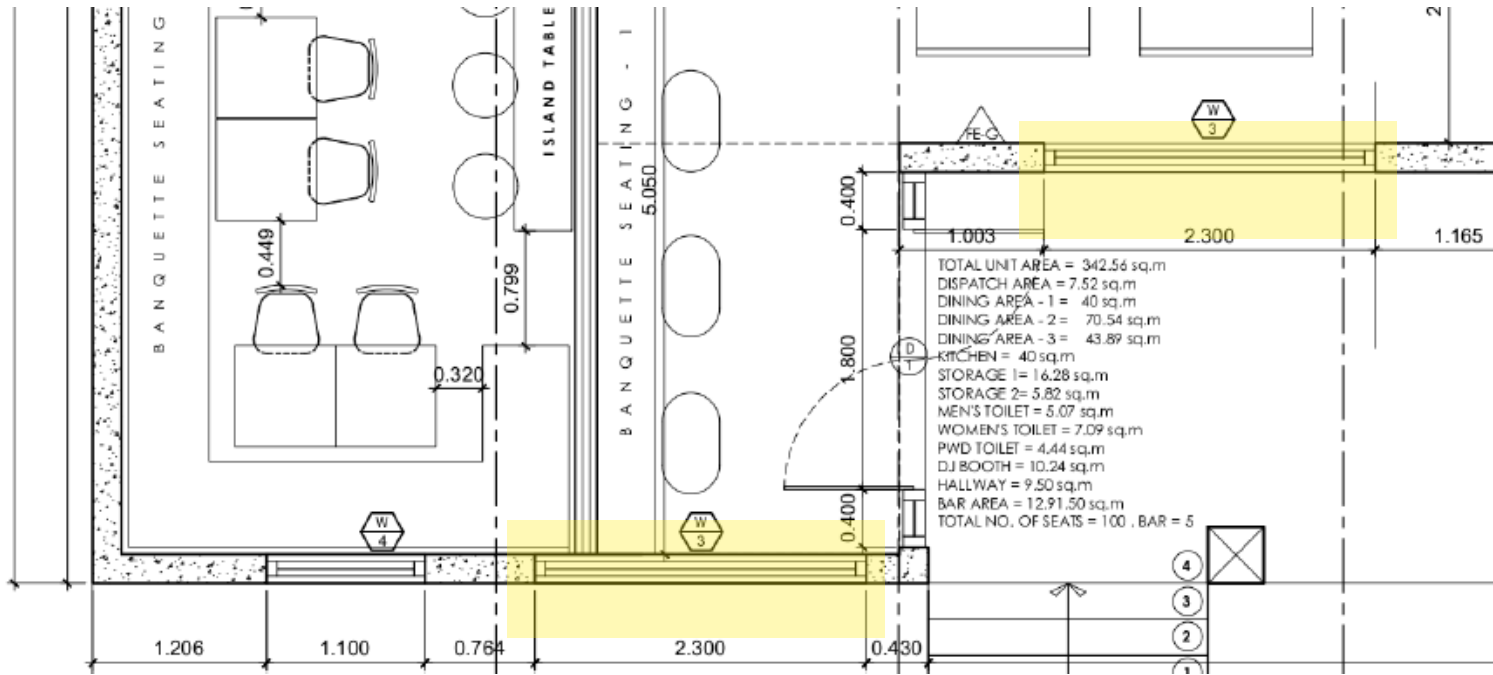


Project: 26-29

Project Location: Pasig City


6) W-4: Small Fixed Round Glass

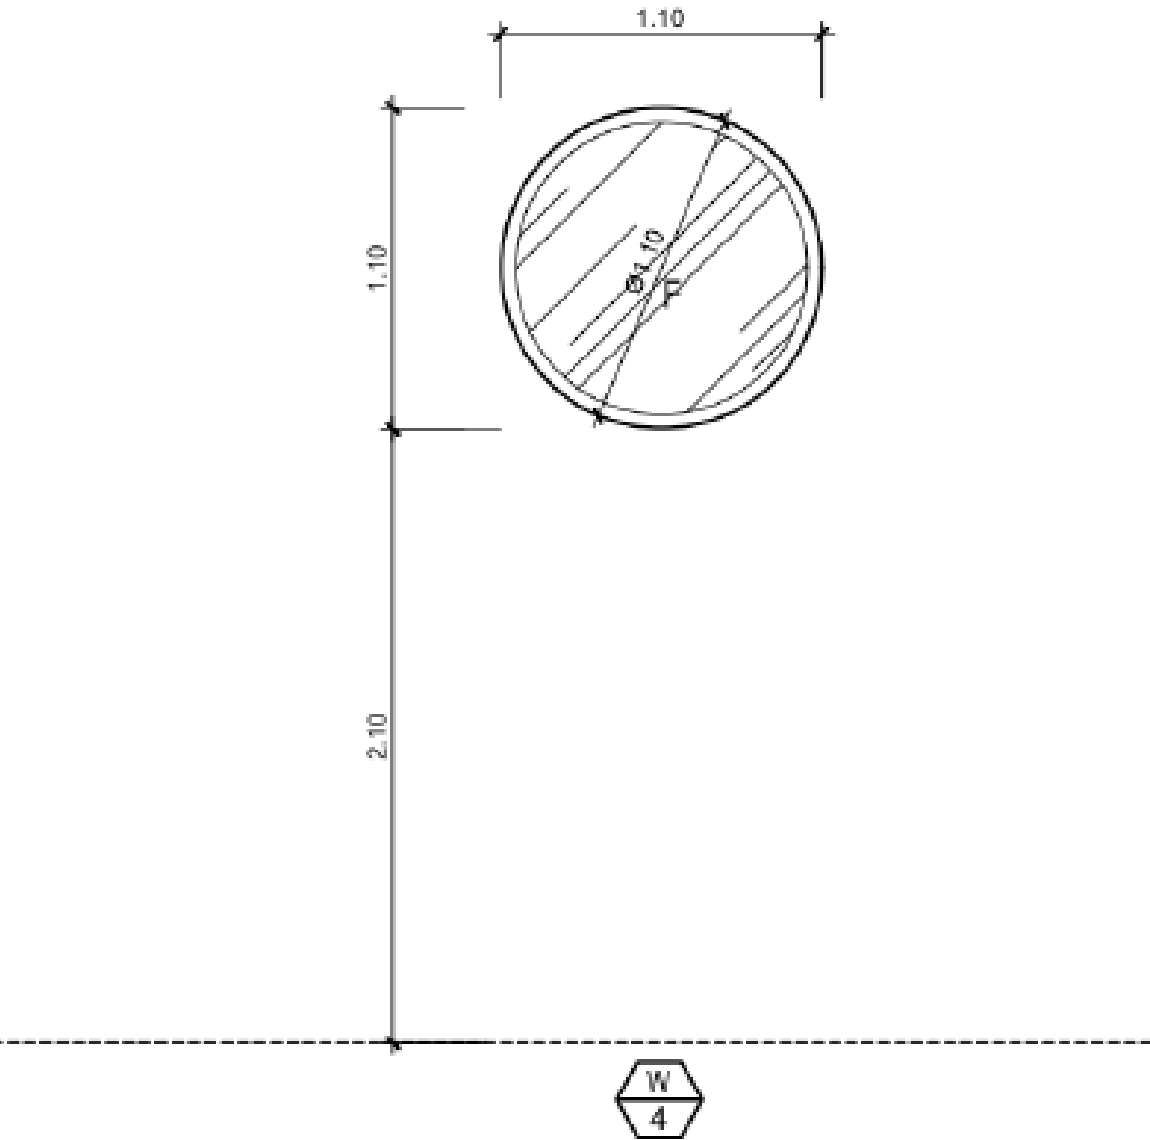

TYPE:	FIXED WINDOW
DESCRIPTION:	12MM THK TEMPERED GLASS WITH 2" x 2" BLACK ANONIZED ALUMINUM FRAMING
LOCATION:	FRONT
REQUIREMENTS:	1 SET

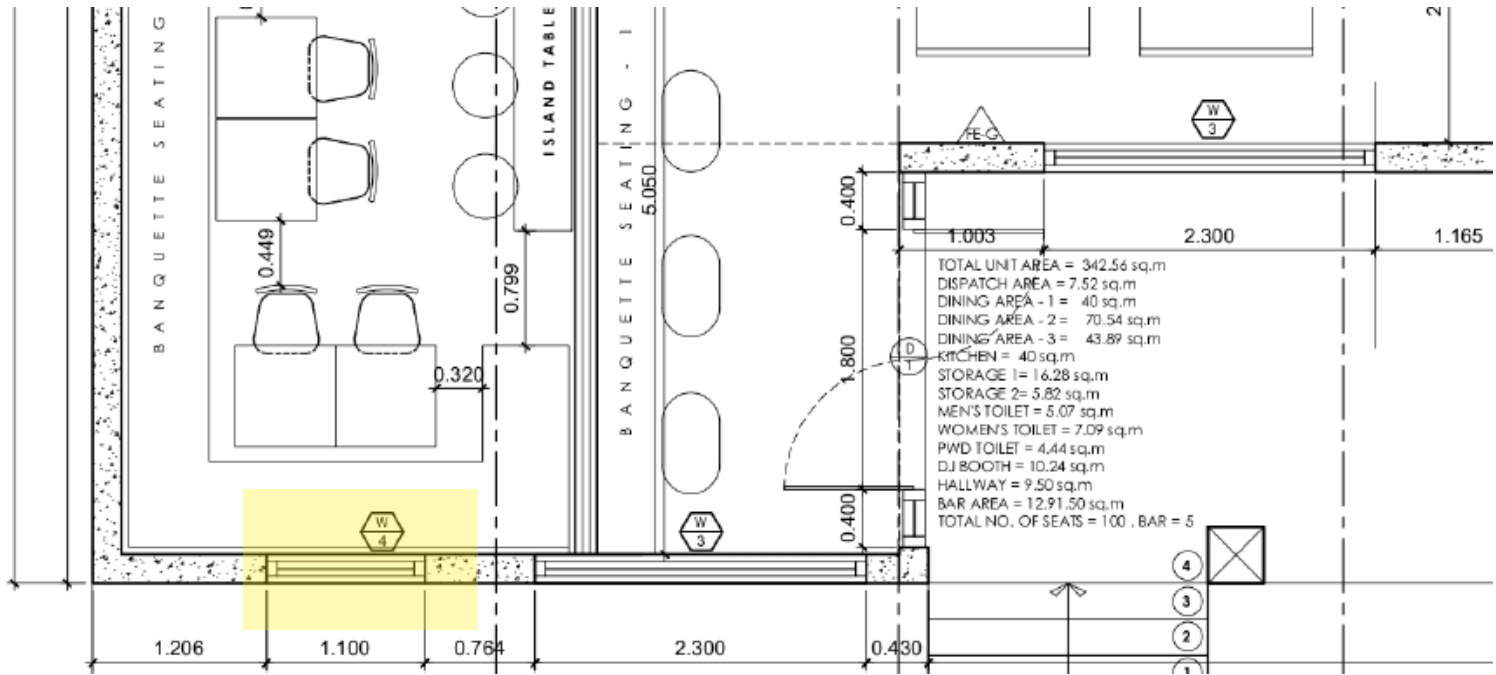


7) GP-1: Partition Glass Wall 1 (4-bay)

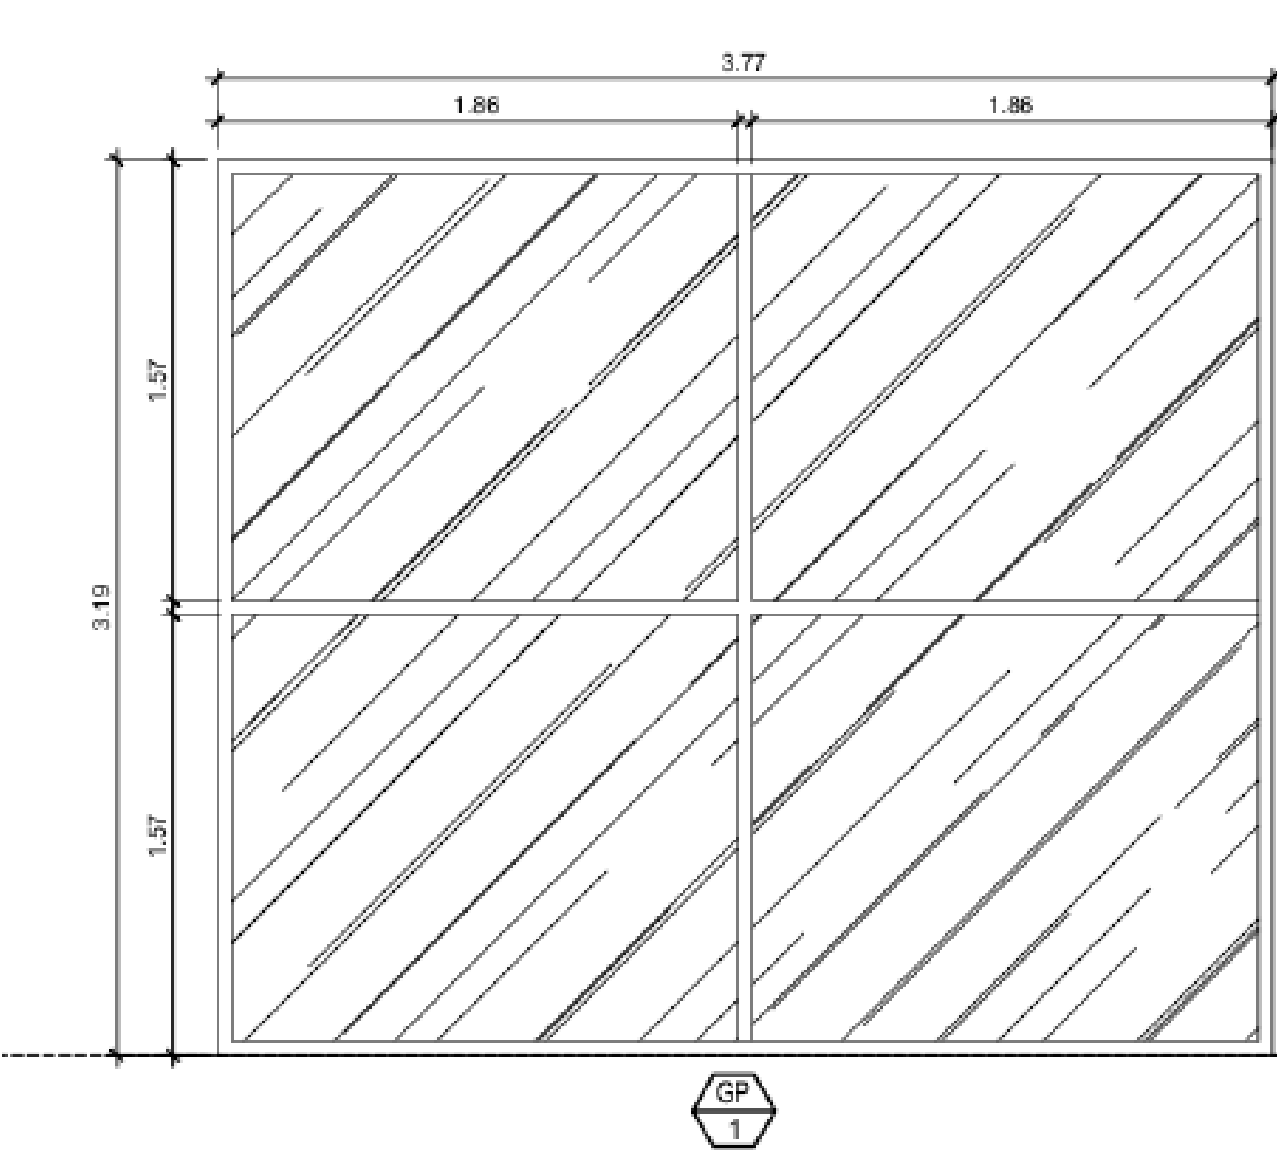


TYPE:	FIXED WINDOW
DESCRIPTION:	12MM THK TEMPERED WITH 2"x2"x1.5mm THK ANONIZED ALUMINUM SATIN BLACK FRAME,
LOCATION:	SMOKING AREA
REQUIREMENTS:	1 SET

8) GP-2: Partition Glass Wall 2 (3-bay)

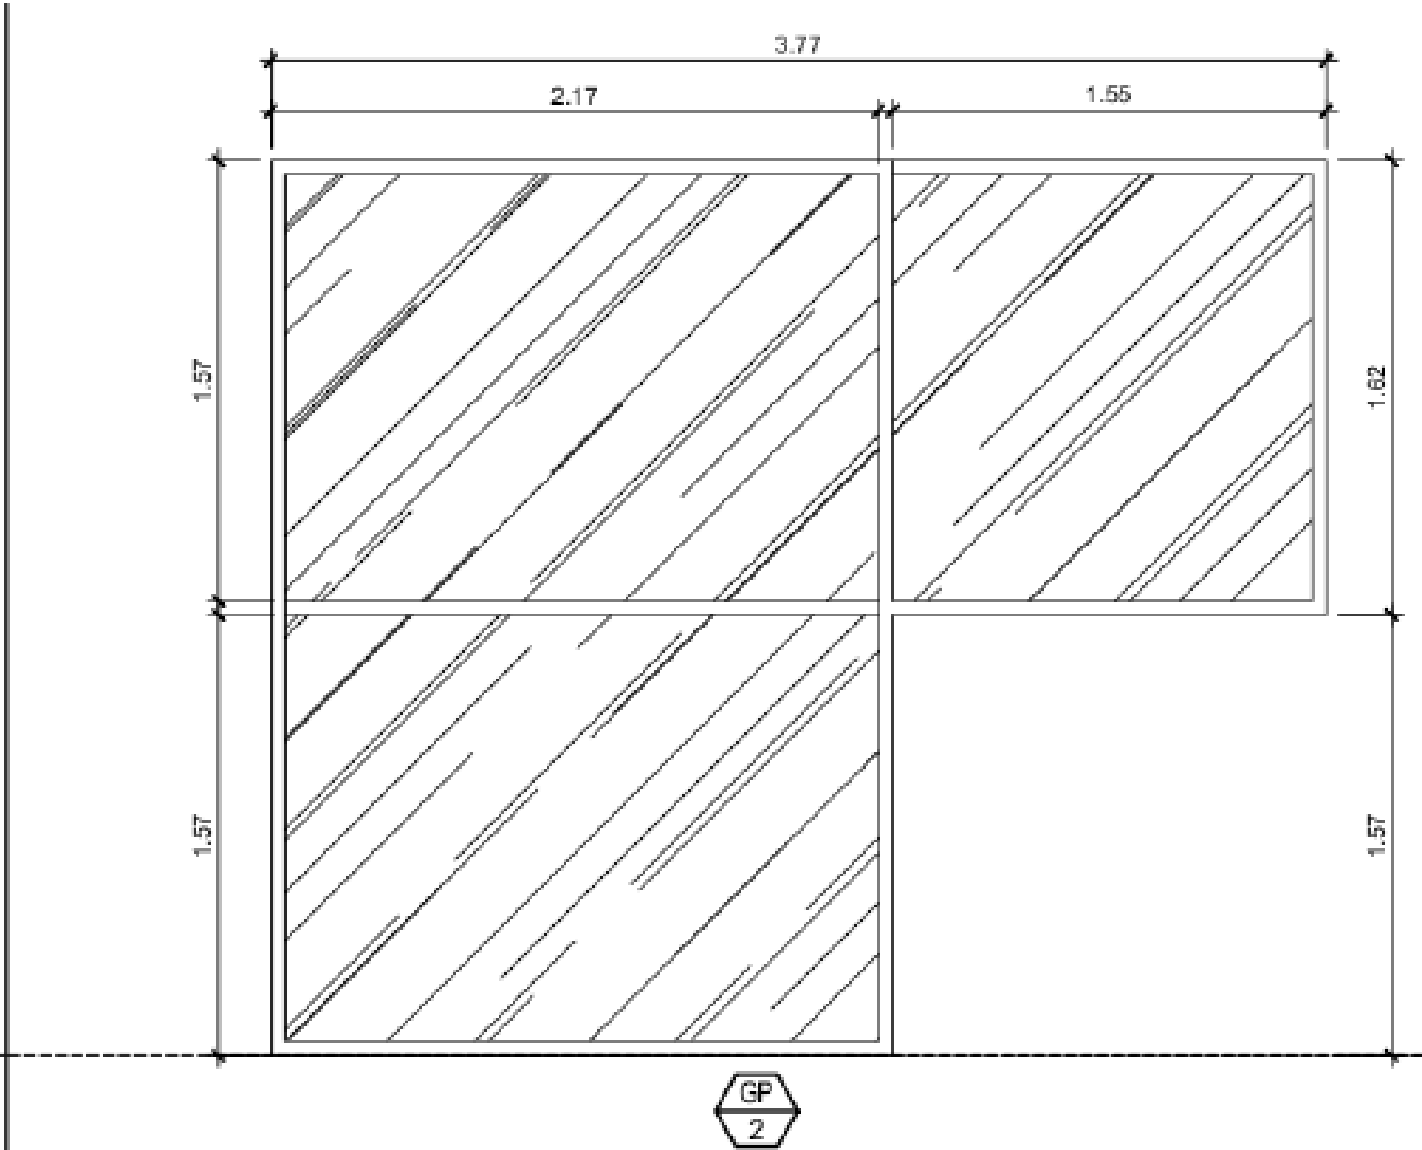

TYPE:	FIXED WINDOW
DESCRIPTION:	12MM THK TEMPERED WITH 2"x2"x1.5mm THK ANONIZED ALUMINUM SATIN BLACK FRAME,
LOCATION:	SMOKING AREA
REQUIREMENTS:	1 SET


ELEVATION

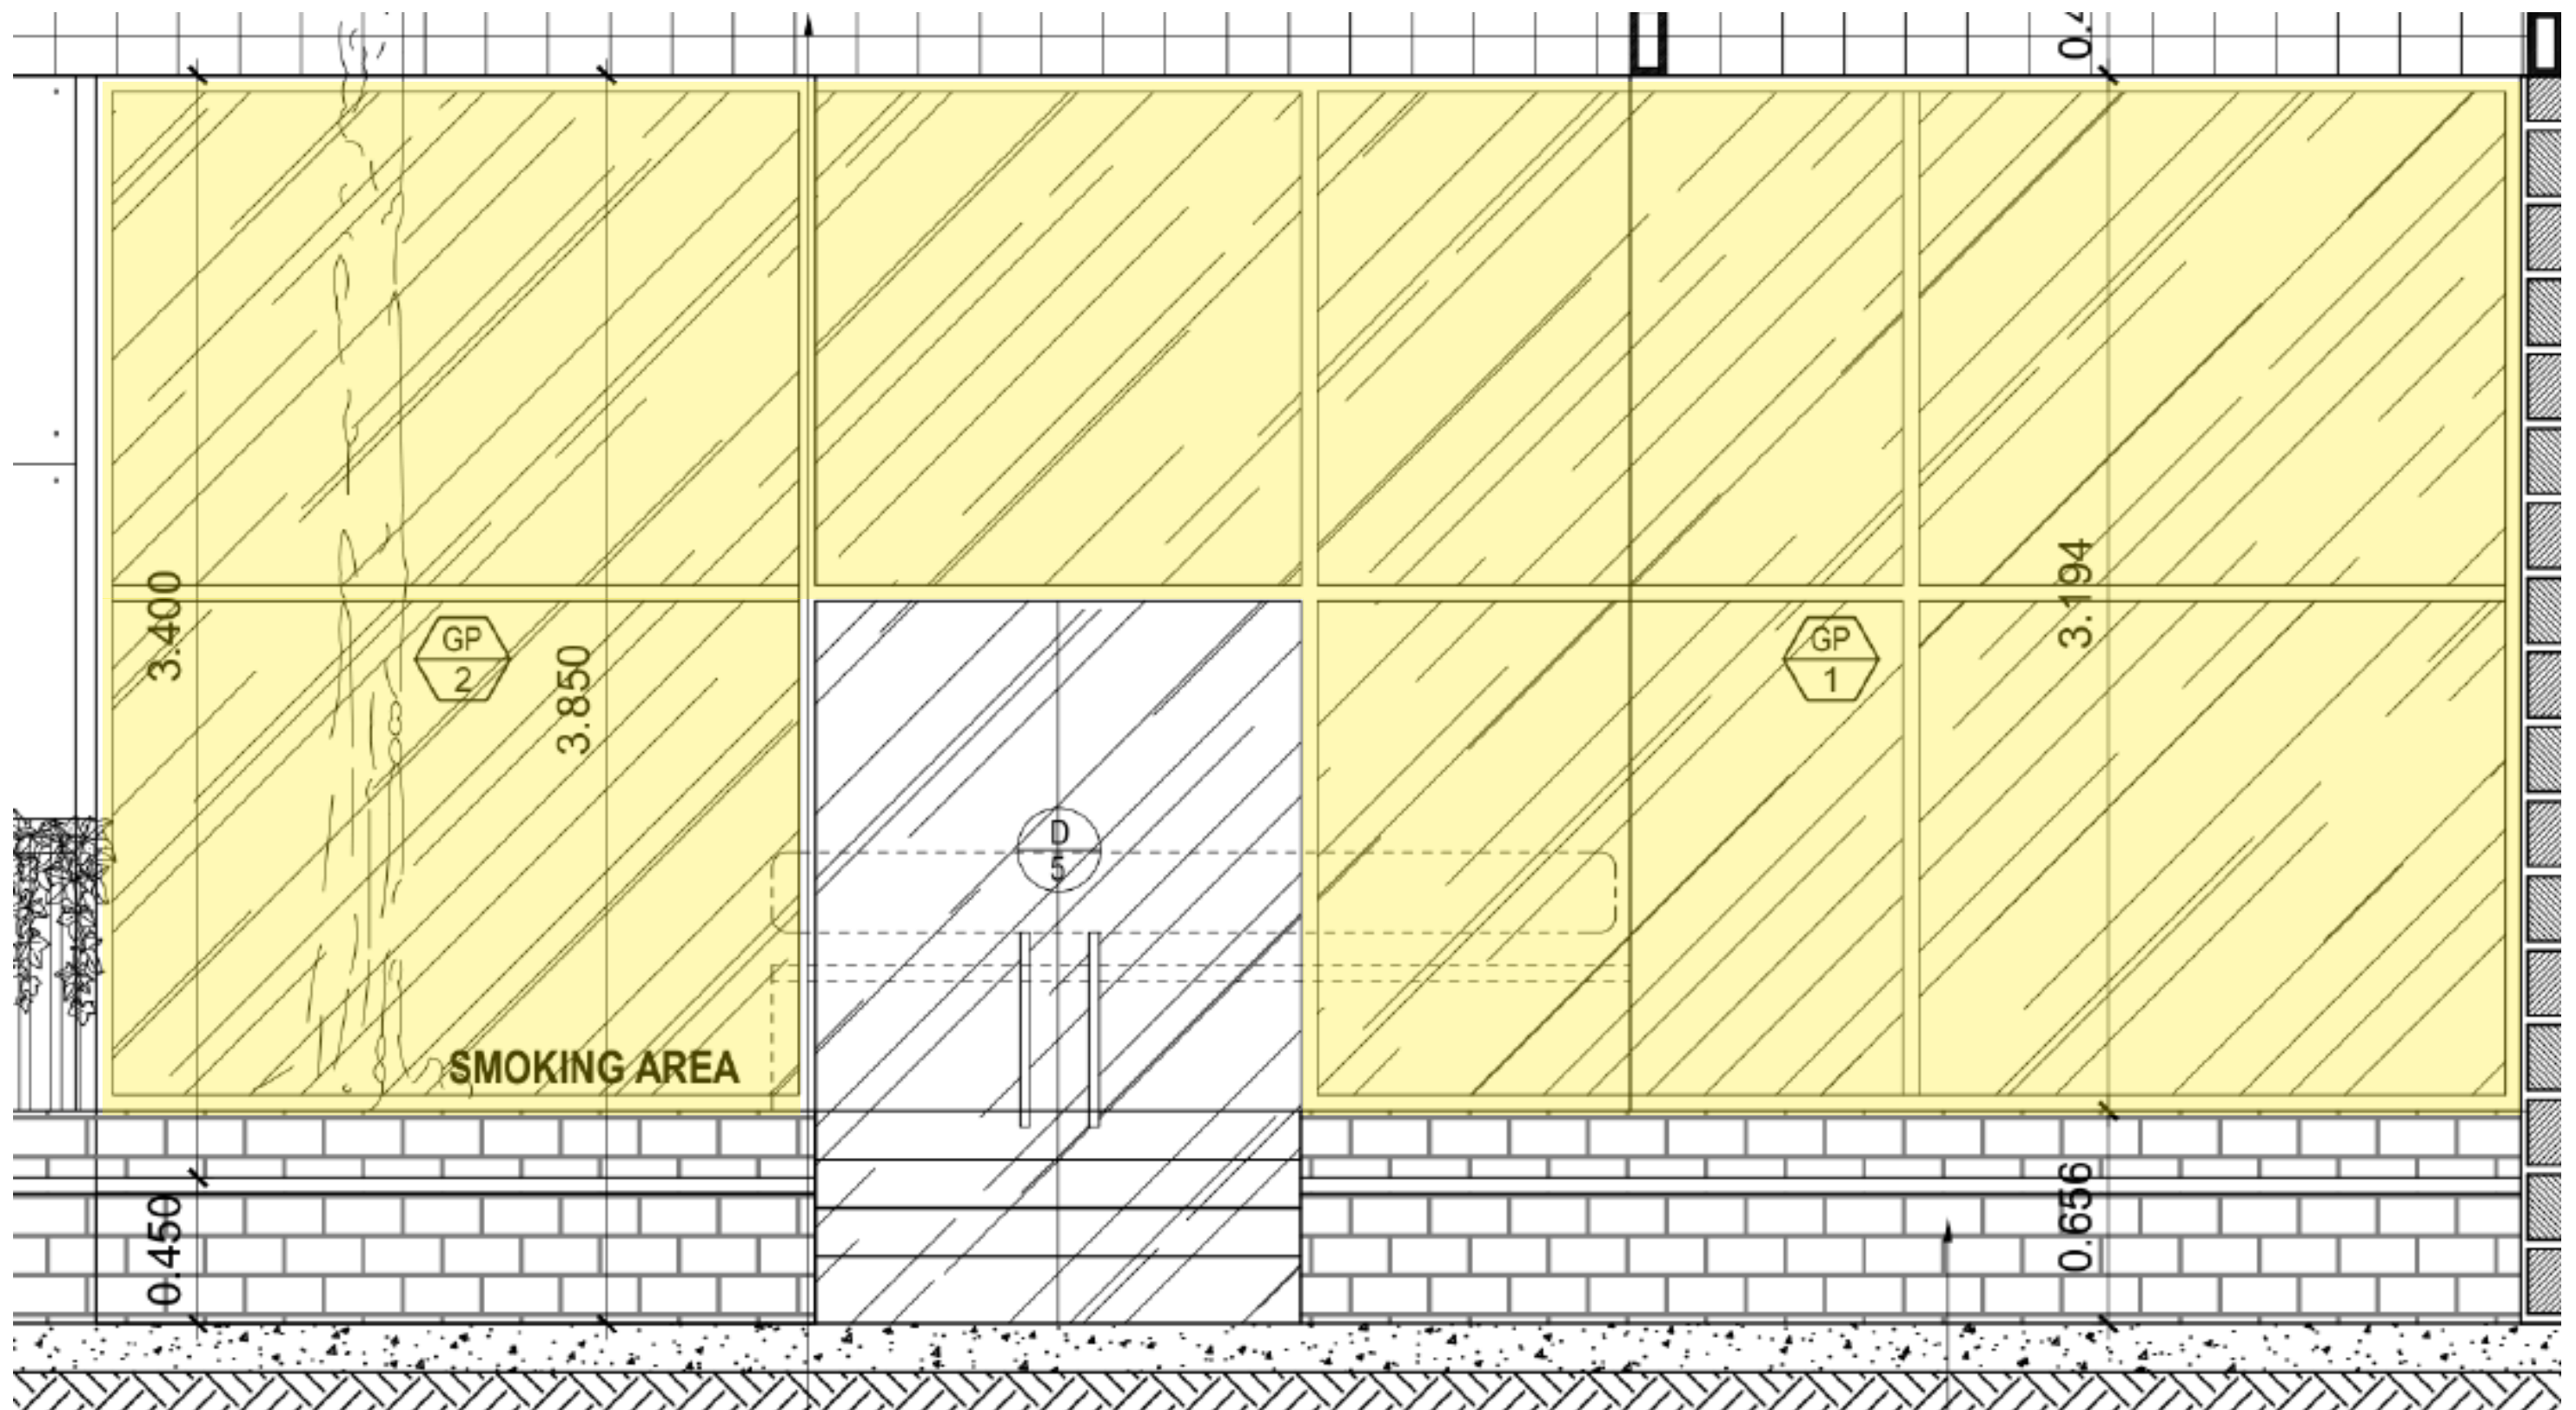


Project: 26-29

Project Location: Pasig City


9) GP-3: Partition Glass Wall 3 (4-bay)

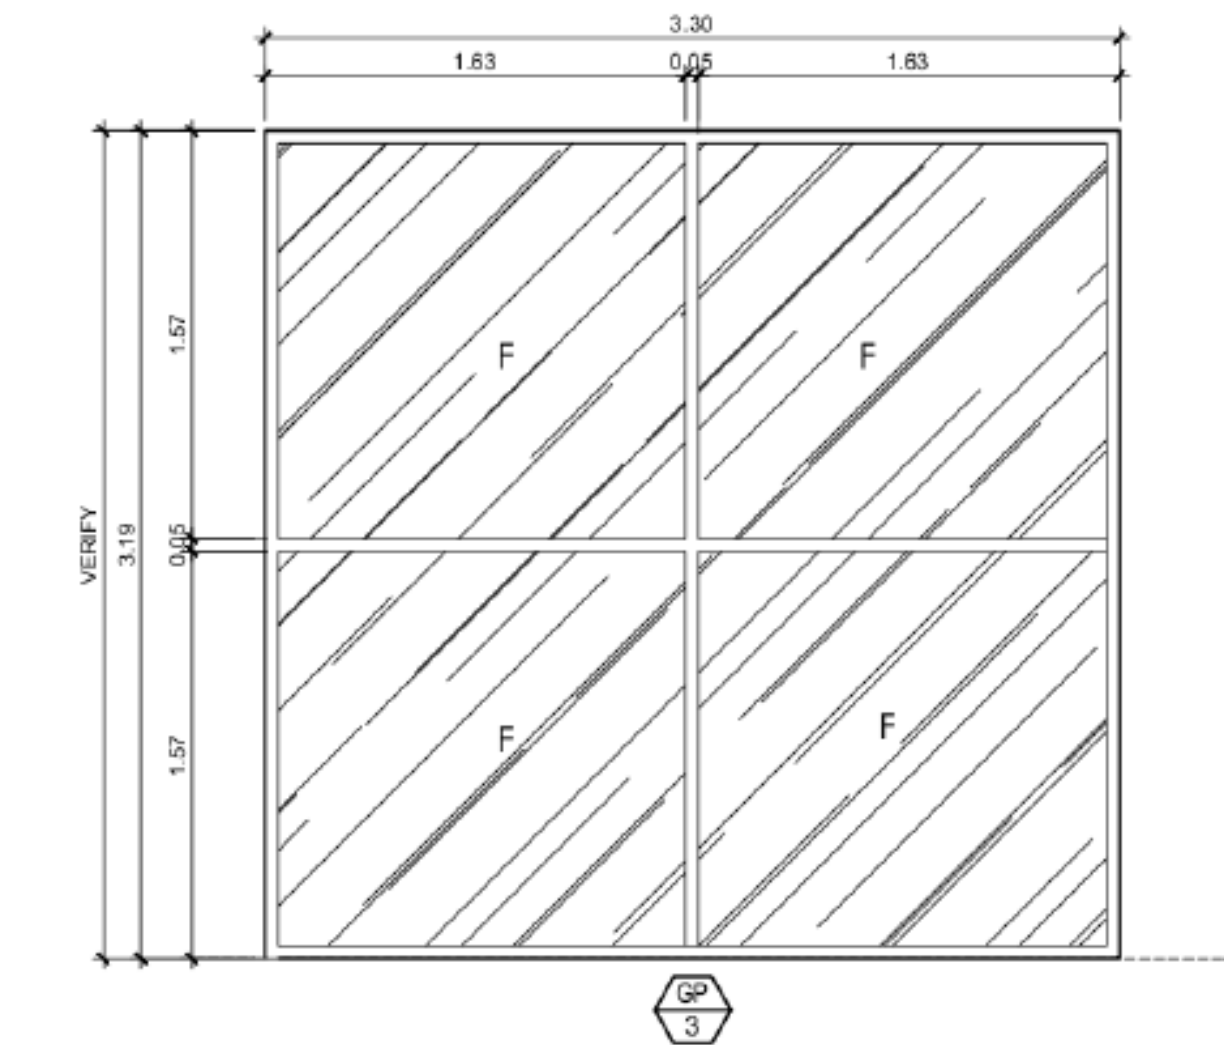

TYPE:	FIXED WINDOW
DESCRIPTION:	12MM THK TEMPERED WITH 2"x2"x1.5mm THK ANONIZED ALUMINUM SATIN BLACK FRAME,
LOCATION:	SMOKING AREA
REQUIREMENTS:	1 SET

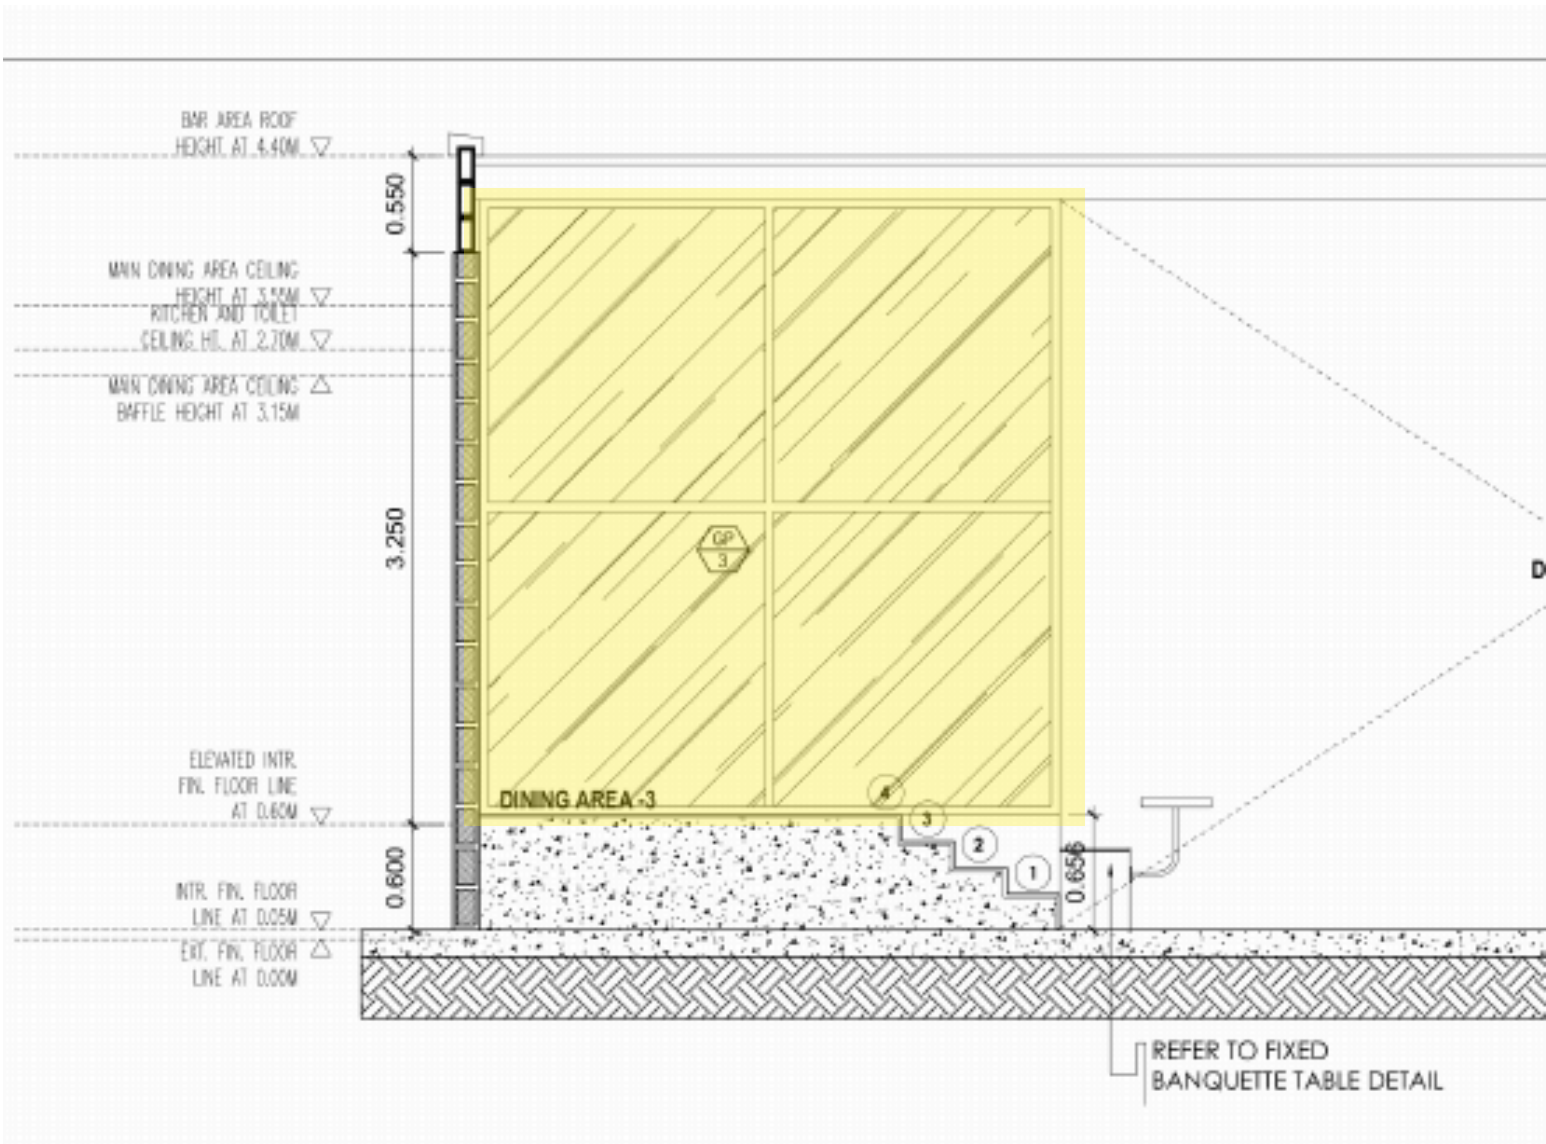


10) GP-4: Partition Glass Wall 4

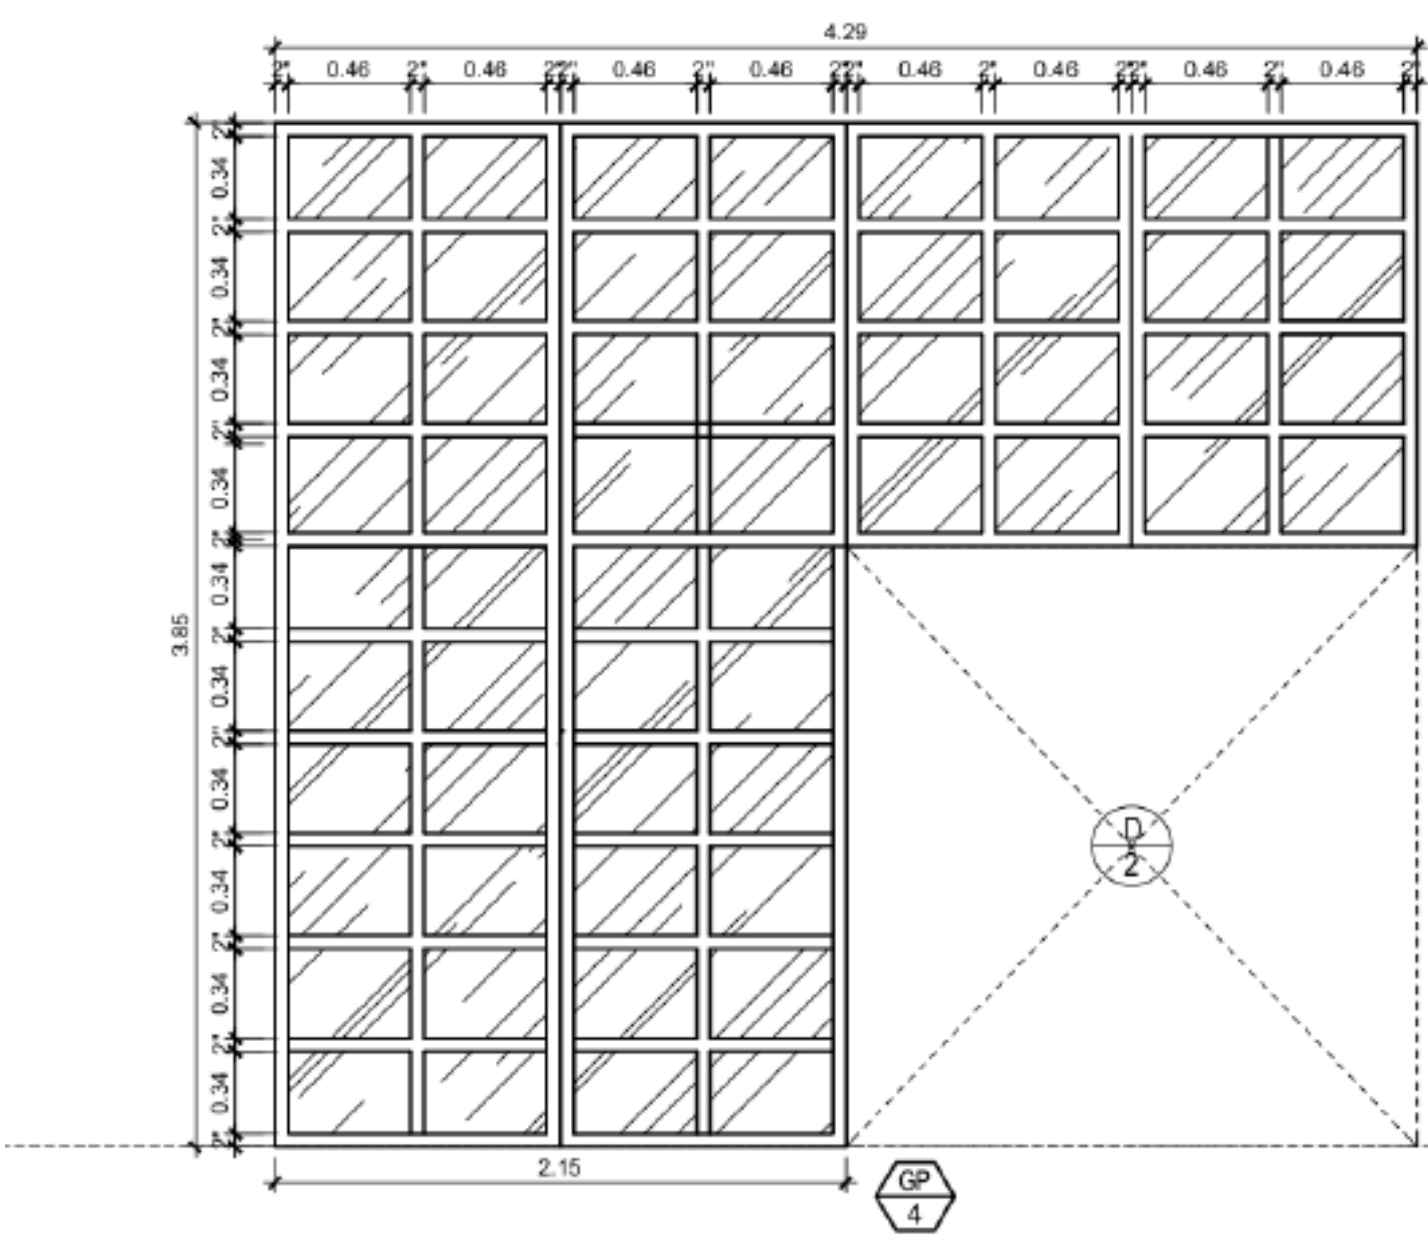


TYPE:	FIXED WINDOW
DESCRIPTION:	12MM THK TEMPERED WITH 2"x2"x1.5mm THK ANONIZED ALUMINUM SATIN BLACK FRAME,
LOCATION:	DINING AREA - 1
REQUIREMENTS:	1 SET

11) GP-5: Partition Glass Wall 5

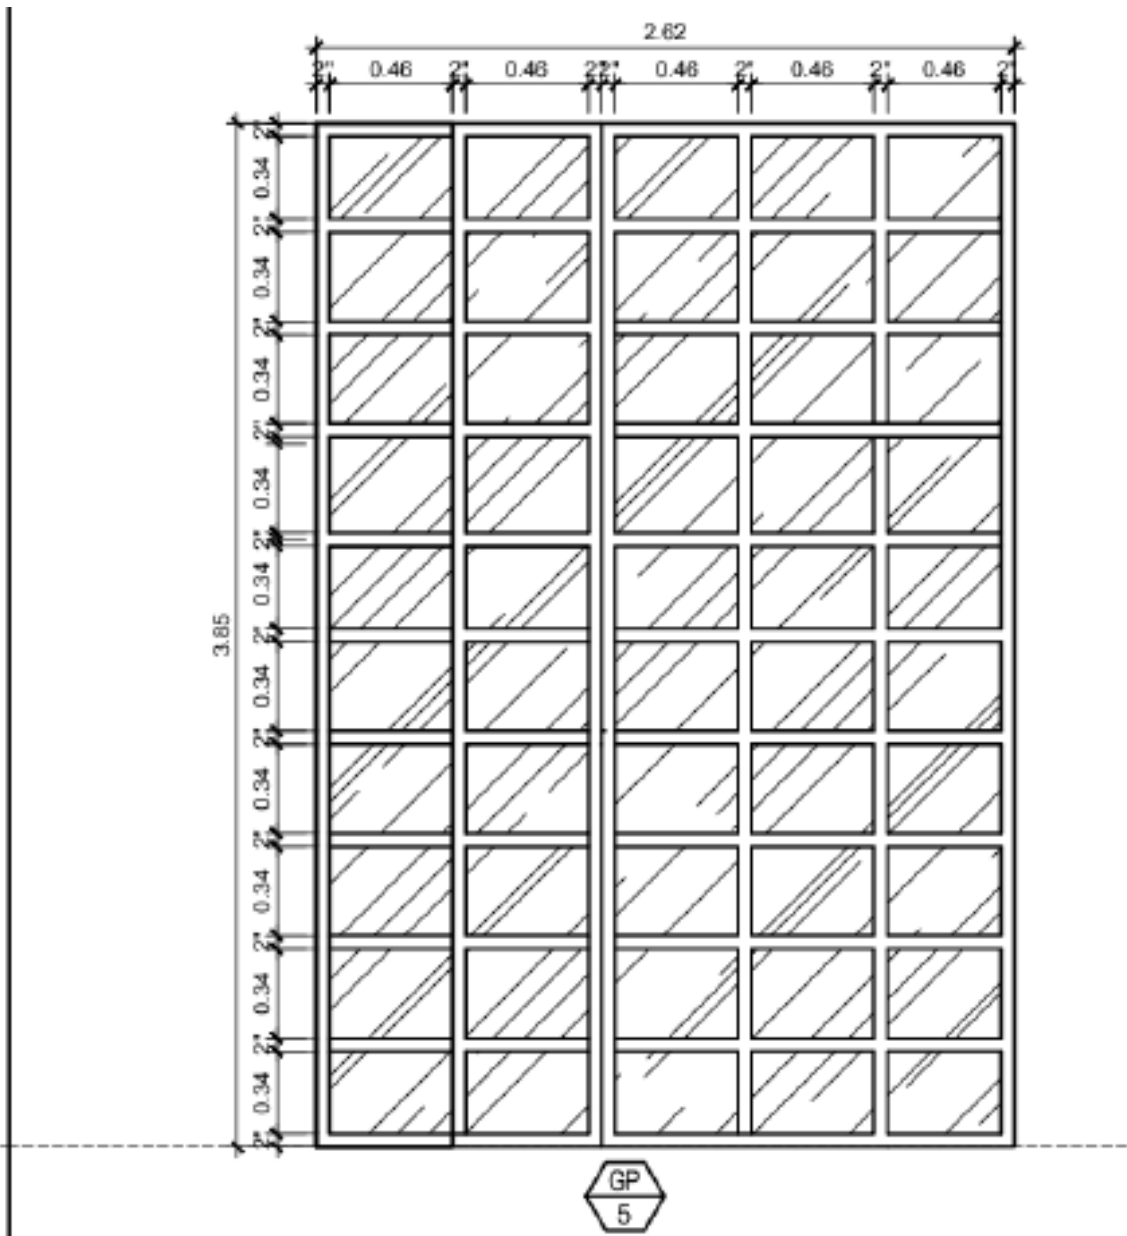

TYPE:	FIXED WINDOW
DESCRIPTION:	12MM THK TEMPERED WITH 2"x2"x1.5mm THK ANONIZED ALUMINUM SATIN BLACK FRAME,
LOCATION:	DINING AREA - 1
REQUIREMENTS:	1 SET


ELEVATION

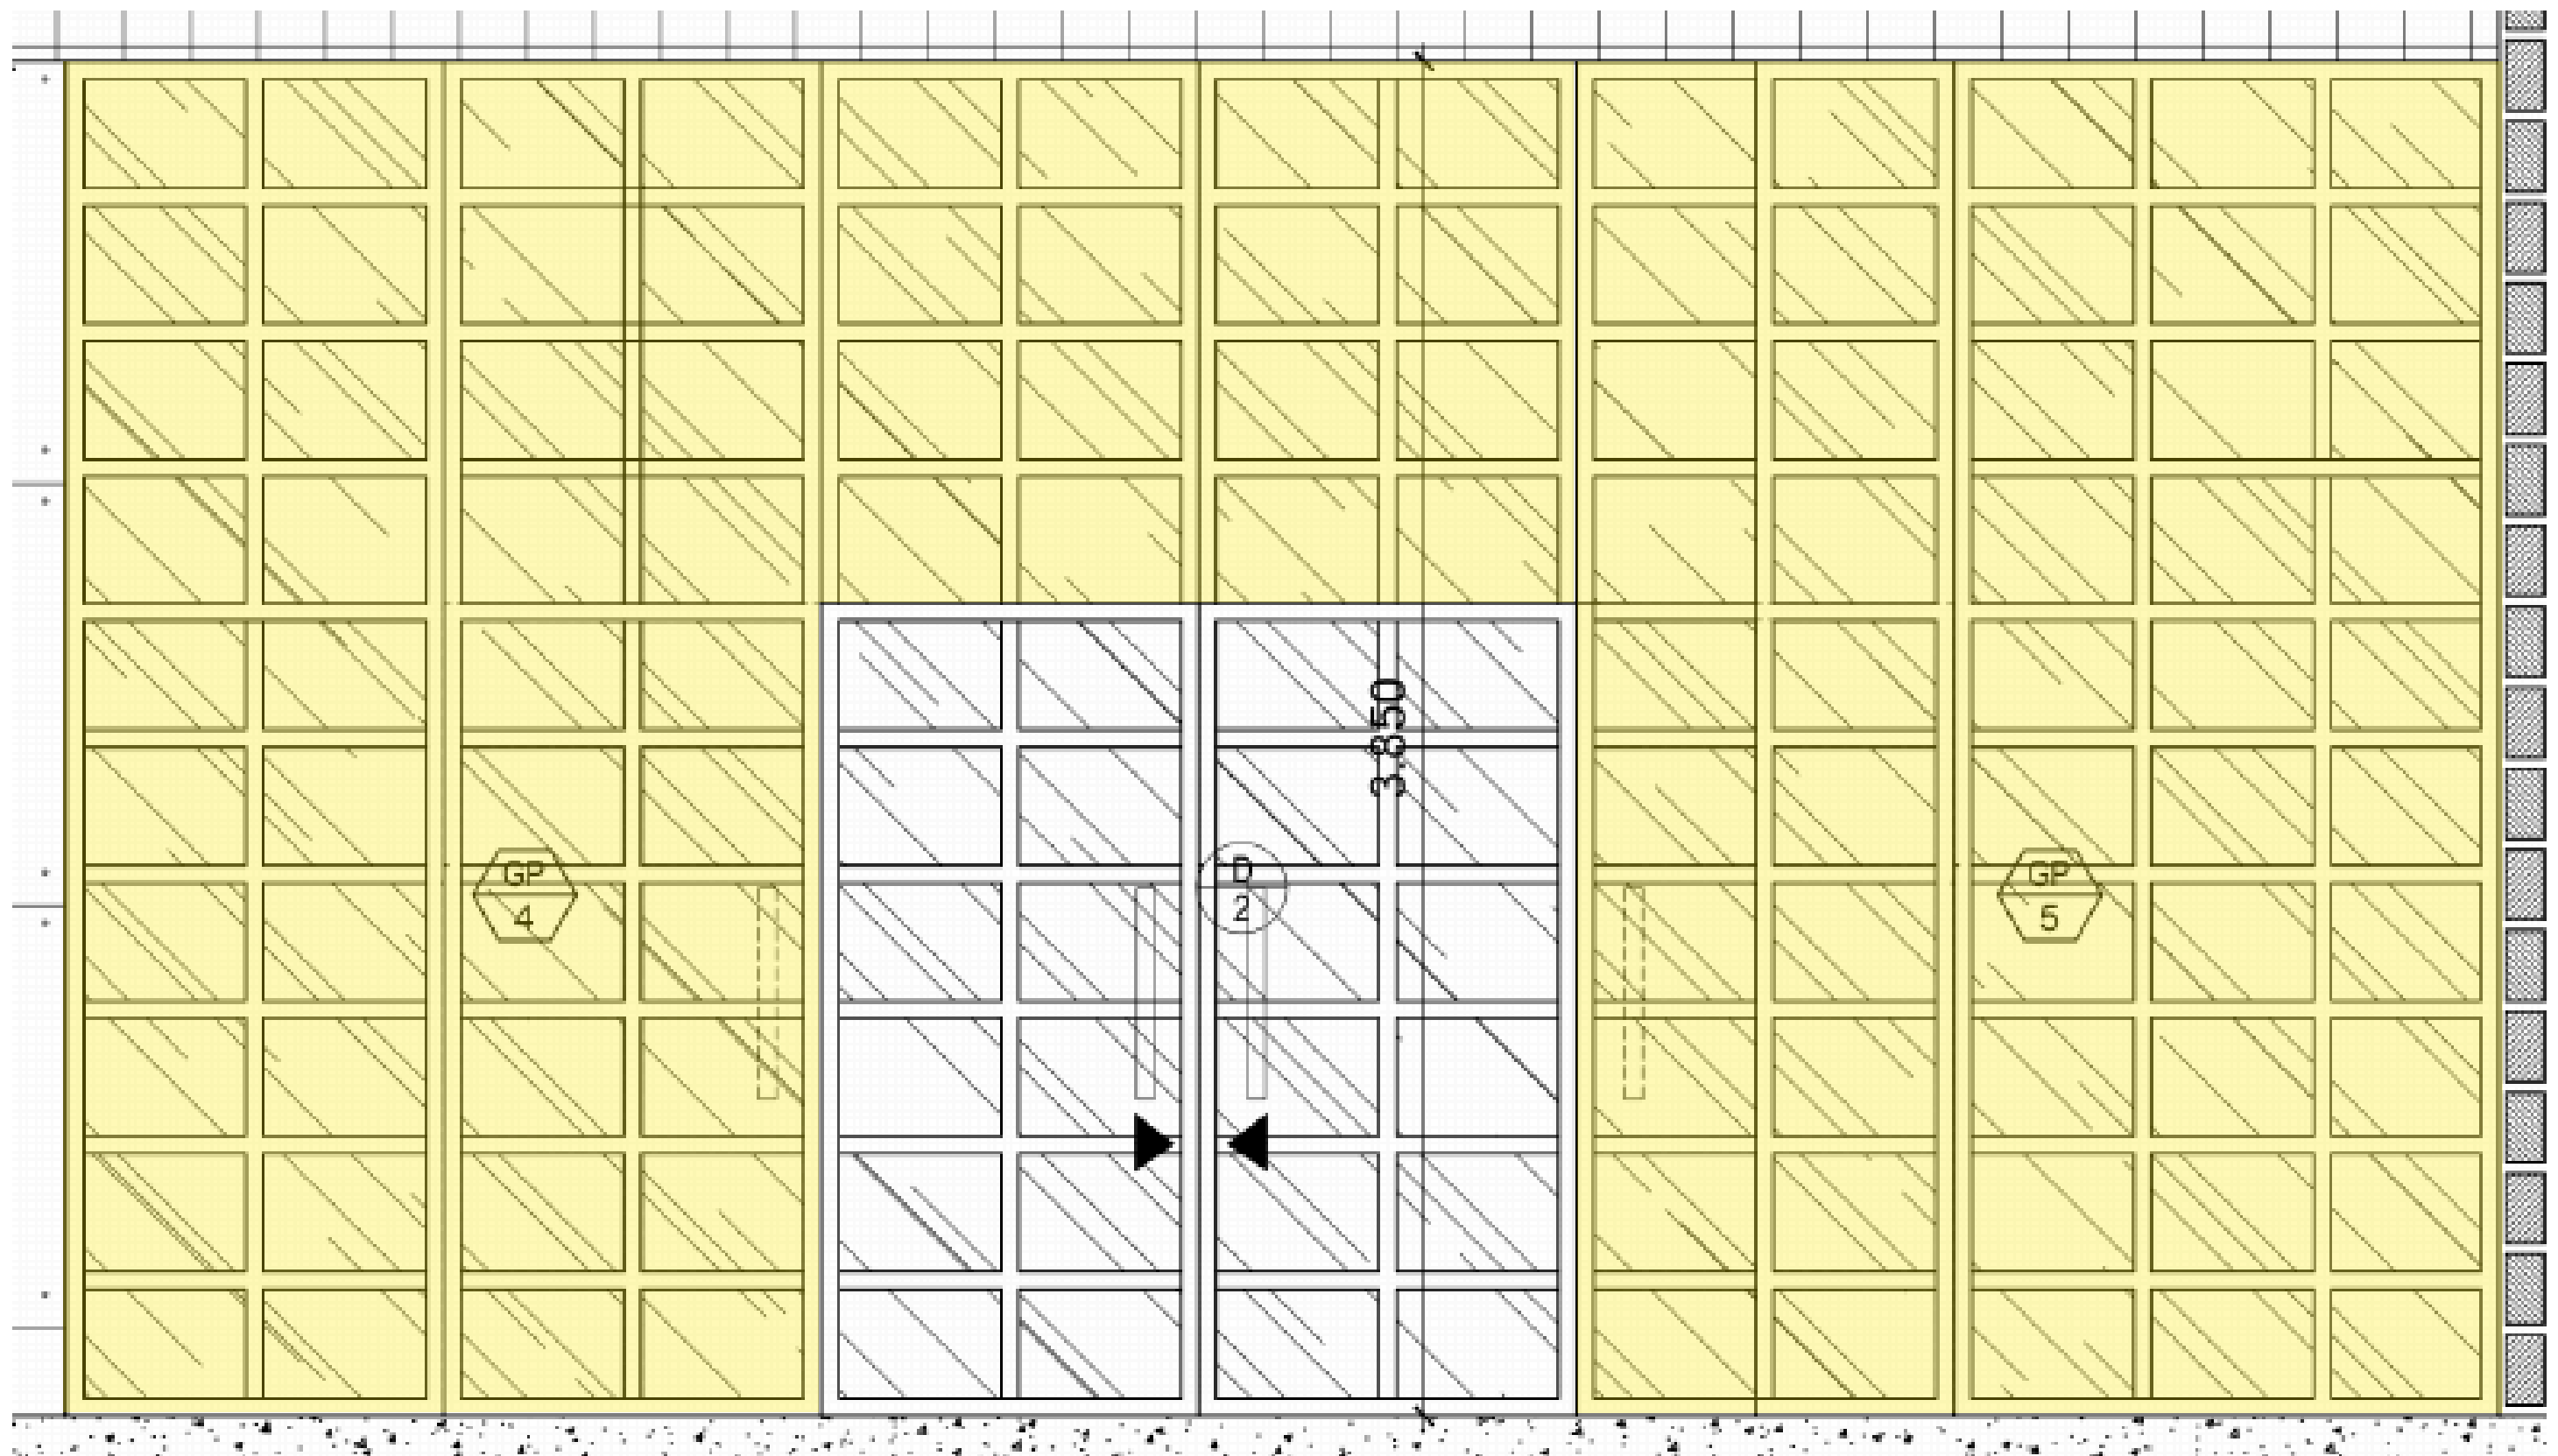

Project: 26-29

Project Location: Pasig City

12) MR-1: Round Mirror

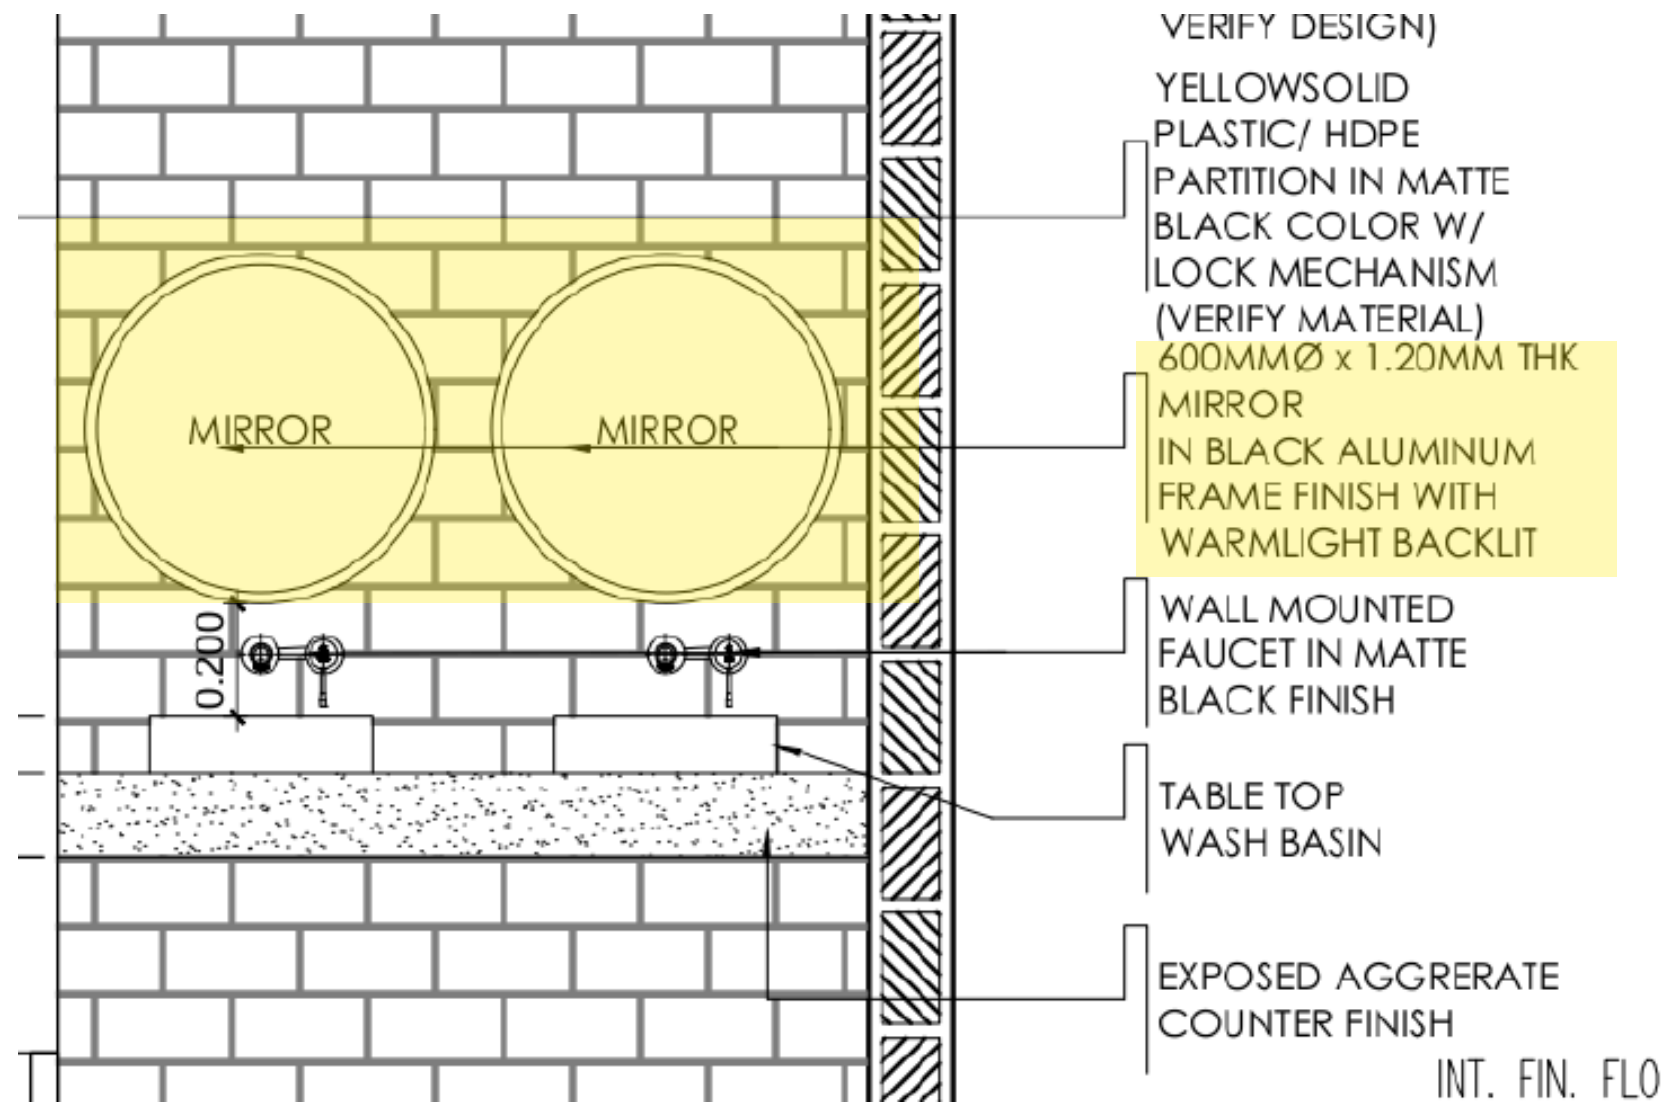

Note: Provide Provision for Striplight

Qty: 3 pcs.