


Project: 26-29


Project Location: Pasig City

1.) D-3: Metal Swing Door with Round Glass

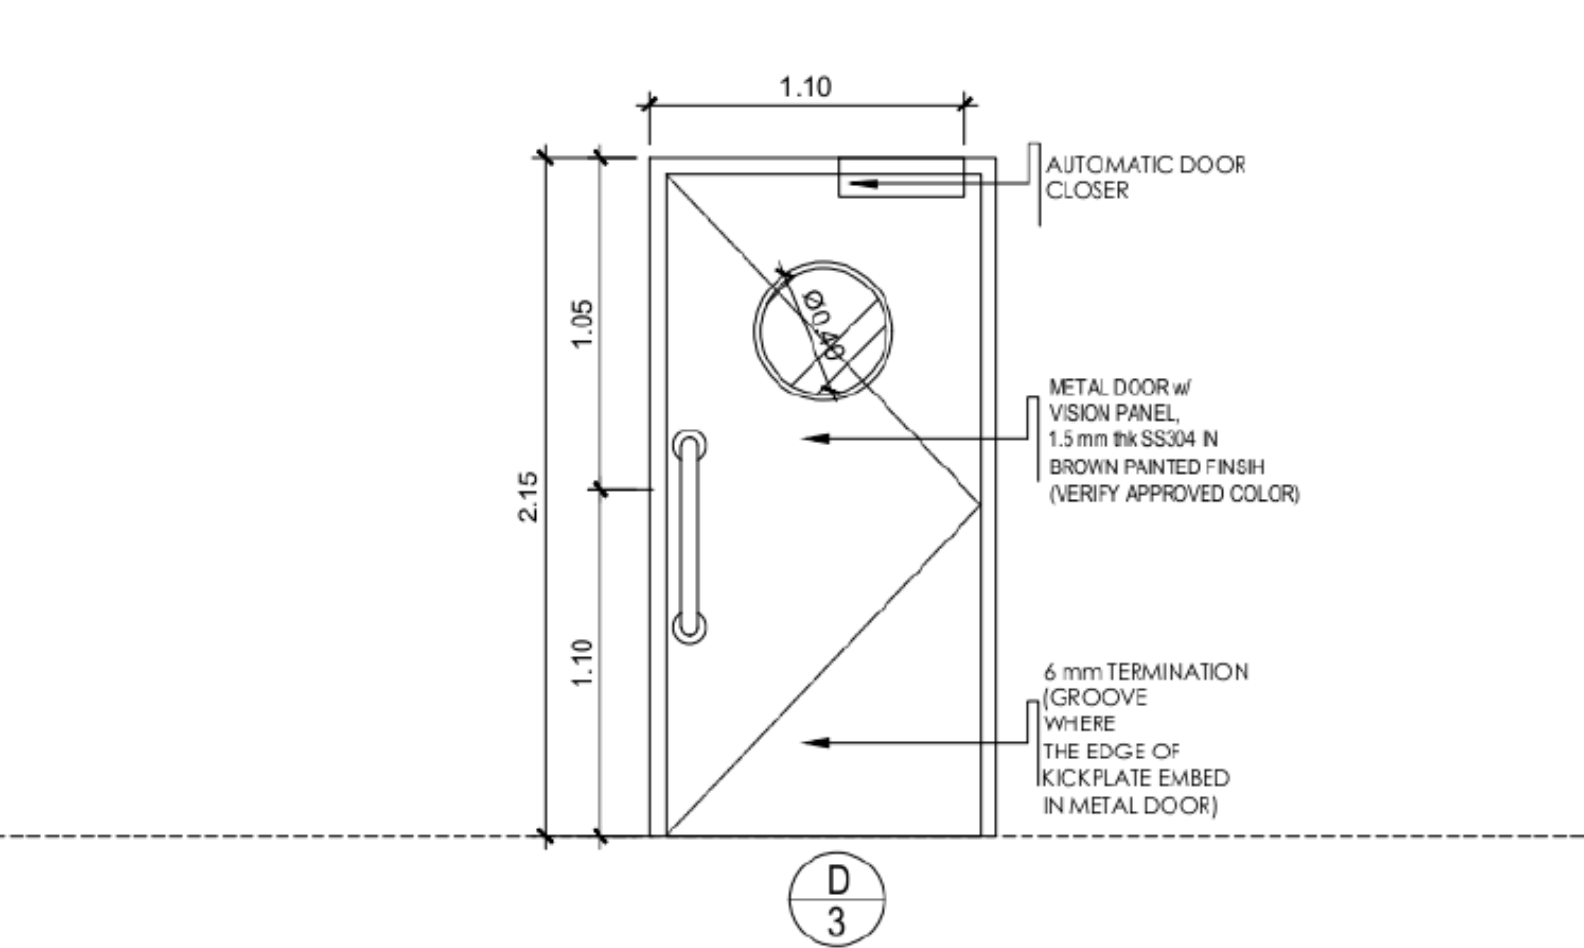

TYPE:	SWING DOOR
DESCRIPTION:	1.2MM THK. METAL FLUSH DOOR W/ VISION PANEL, 1.2MM THK. STAINLESS STEEL 304 HAIRLINE FINISH KICK PLATE (1.10M HIGH) AND DOOR HANDLE ON BOTH SIDES
LOCATION:	KITCHEN DOOR
REQUIREMENTS:	2 SET

REQUIREMENTS:

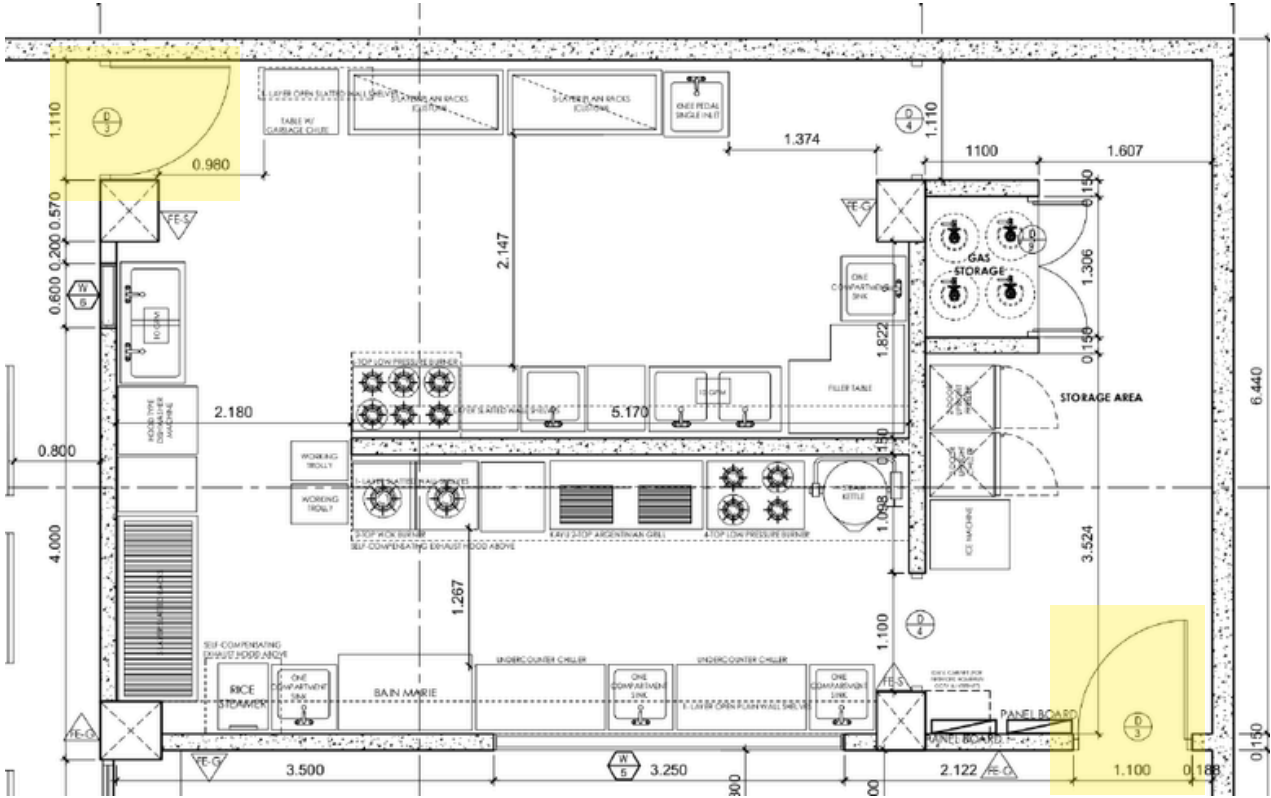


Note:

- Include Round Glass if available, if NOT available, please provide provision for glass
- Include all accessories and hardwares


Project: 26-29

Project Location: Pasig City

2.) D-4: Metal Door Jamb

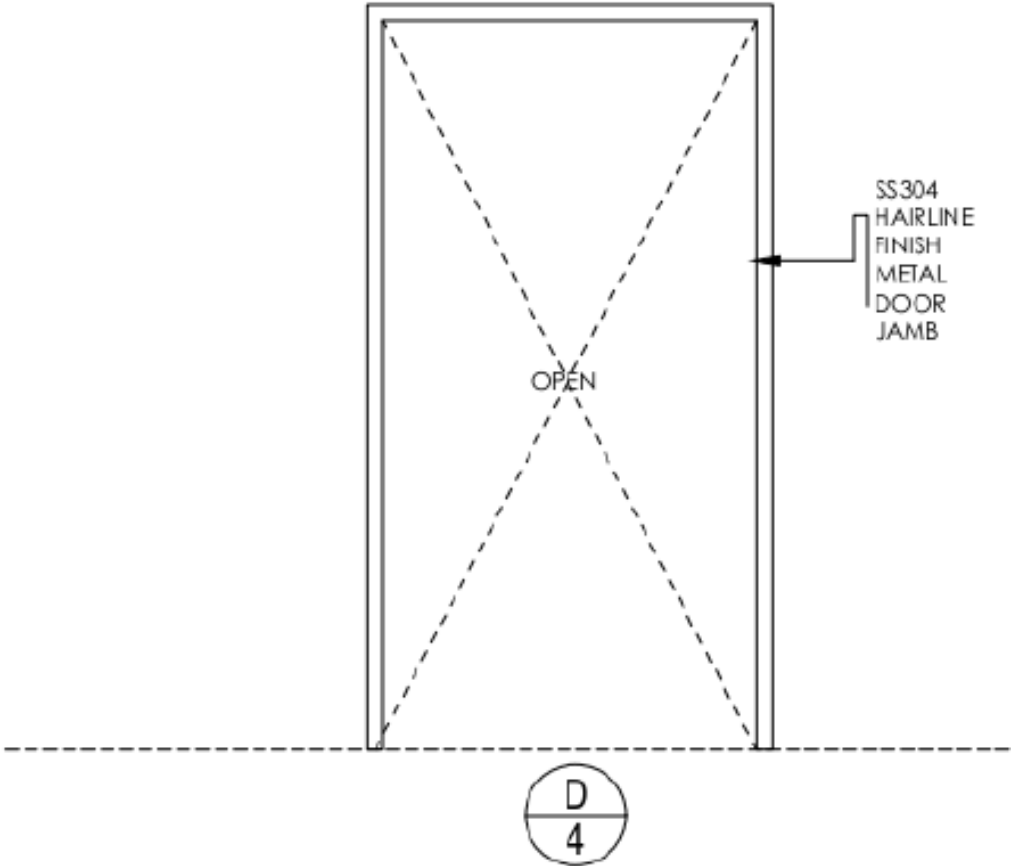

TYPE:	OPEN
DESCRIPTION:	OPEN
LOCATION:	KITCHEN AREA
REQUIREMENTS:	2 SET

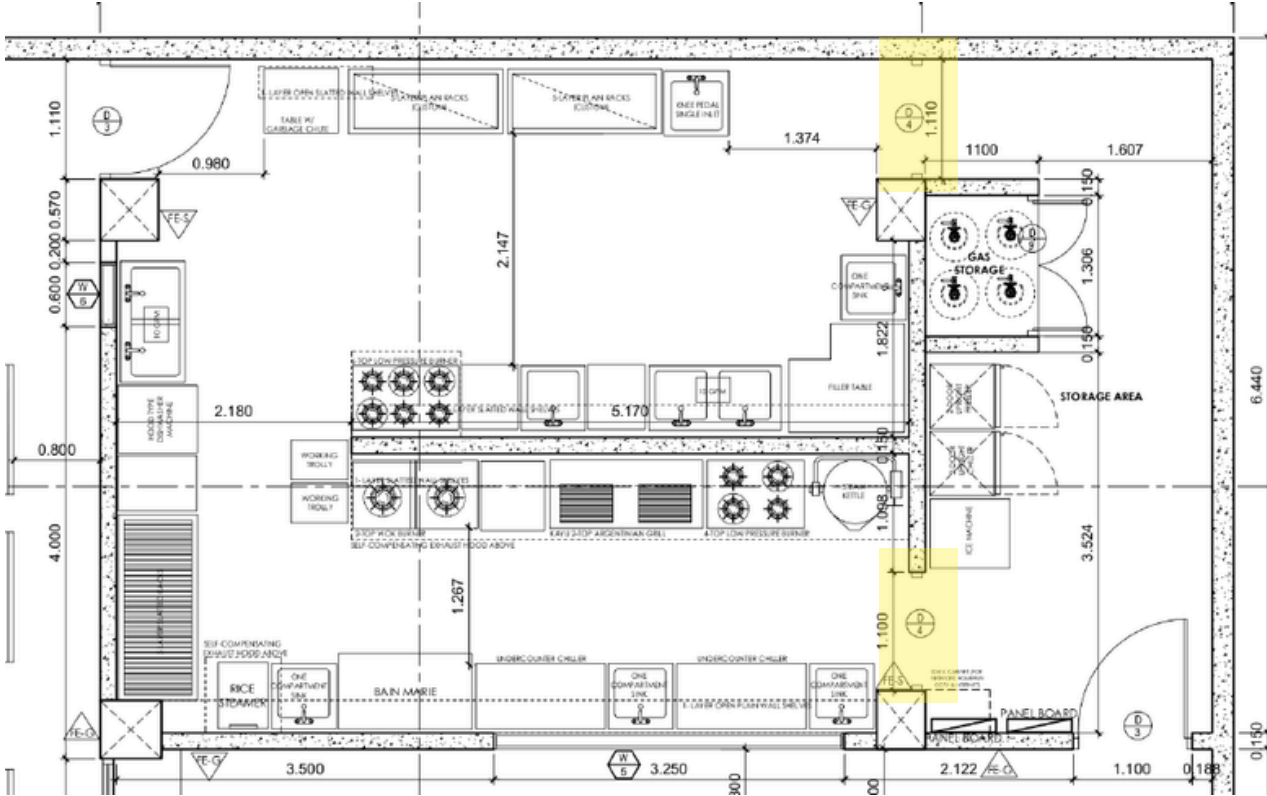


Note:

-Door Jamb only

Project: 26-29


Project Location: Pasig City

3.) D-6: Metal Swing Door

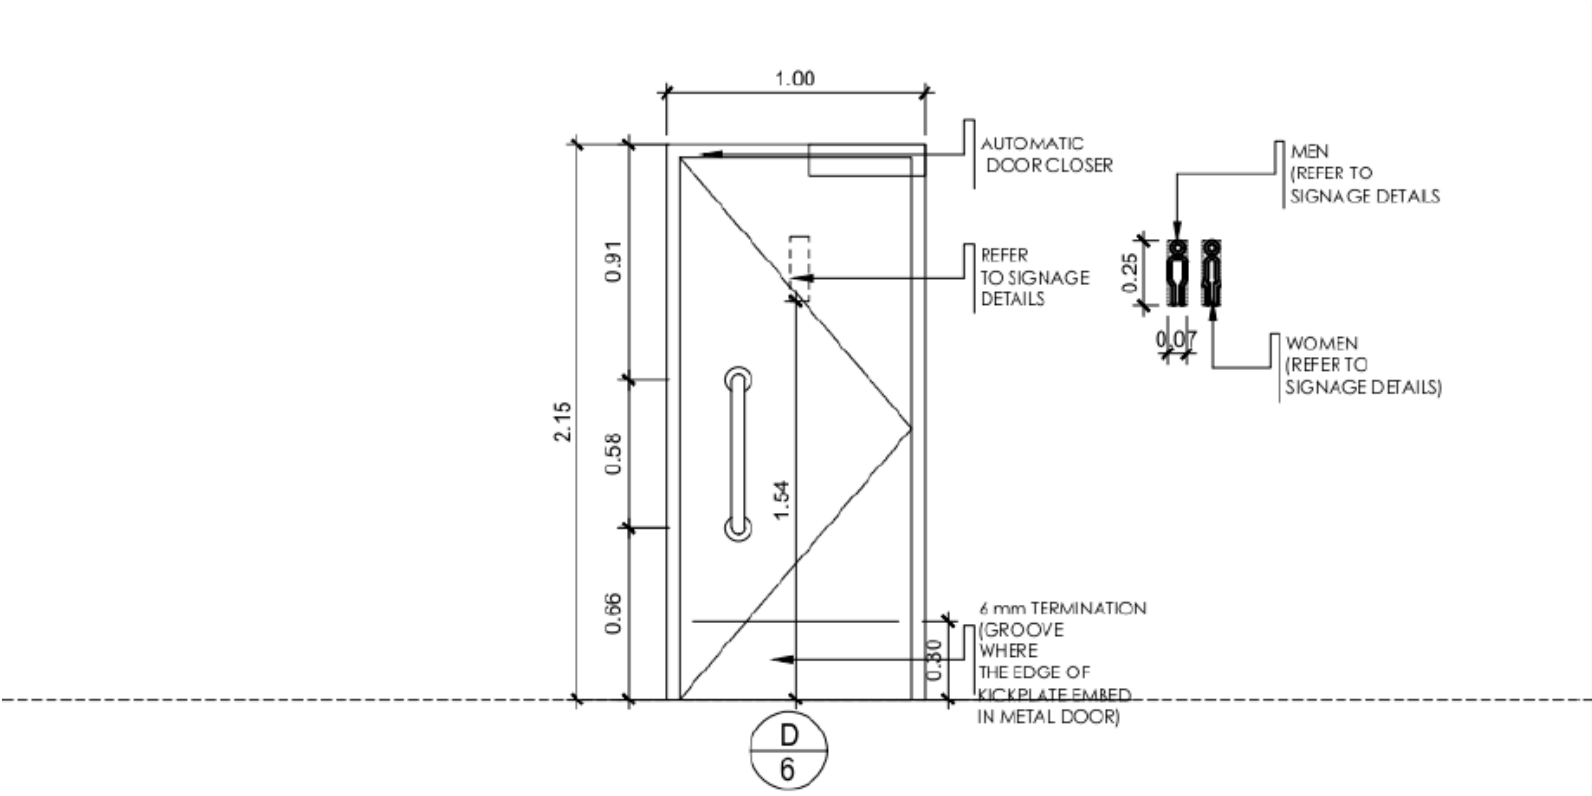

TYPE:	SWING DOOR
DESCRIPTION:	1.2MM THK. METAL FLUSH DOOR W/ 1.2MM THK. STAINLESS STEEL 304 HAIRLINE FINISH KICK PLATE (0.30M HIGH), DOOR HANDLE ON BOTH SIDES, PRIVACY INDICATOR (VACANT / OCCUPIED) DEADBOLT LATCH AND DOOR CLOSER
LOCATION:	MEN AND WOMEN TOILET DOOR
REQUIREMENTS:	2 SET


- Note:
- Exclude the signage
 - Include all accessories and hardwares

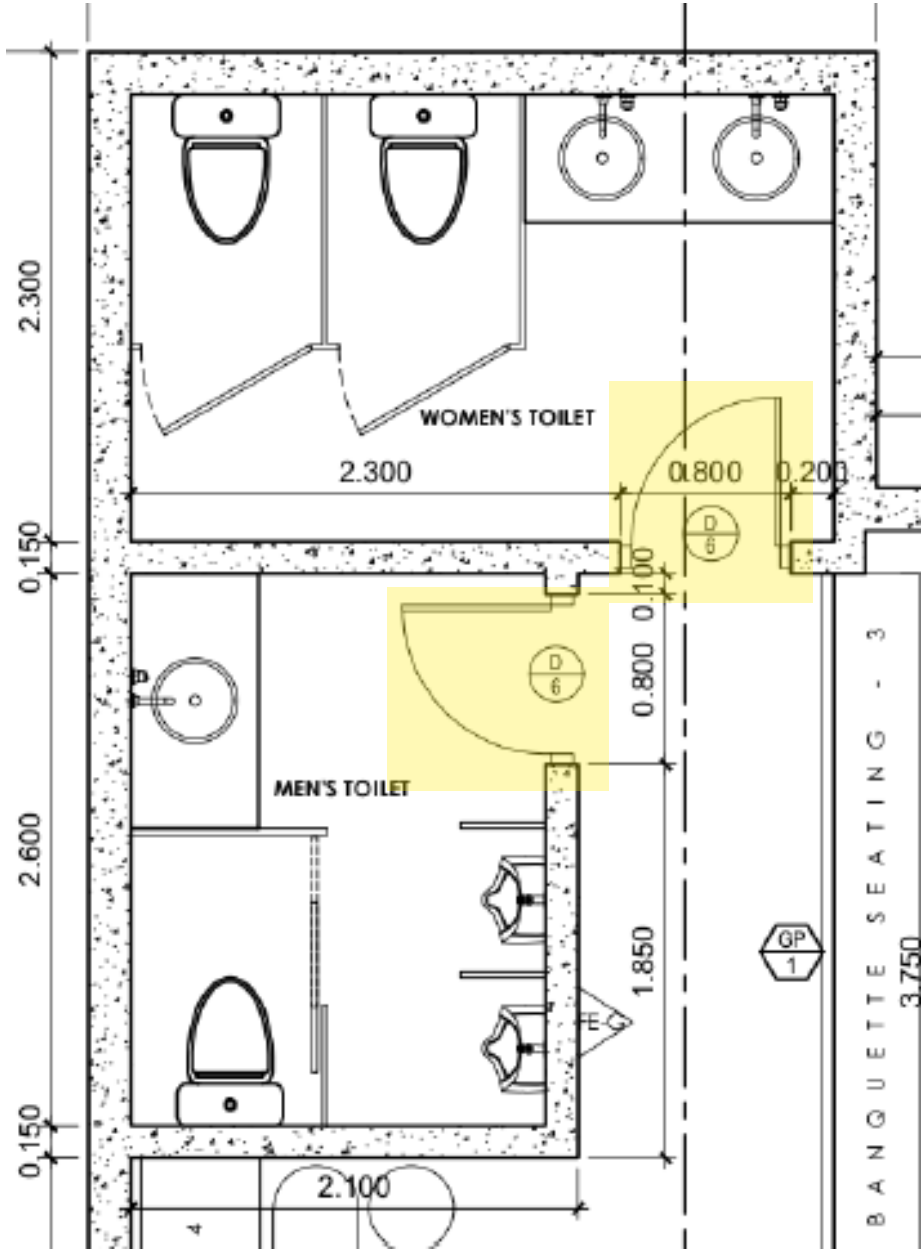

Project: 26-29


Project Location: Pasig City

4.) D-7: Metal Swing Door

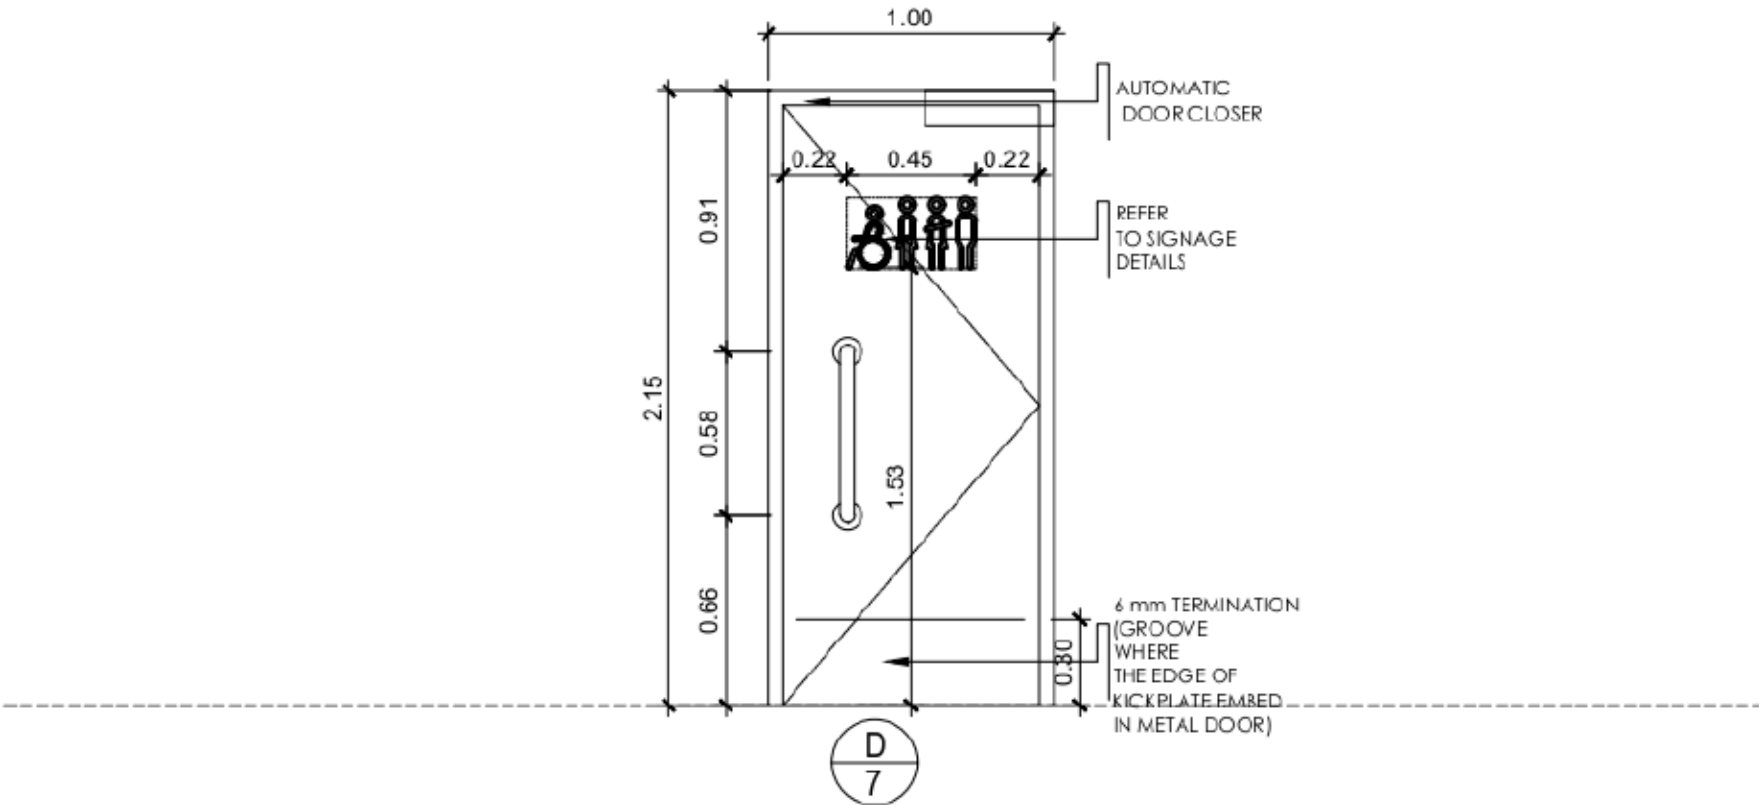

TYPE:	SWING DOOR
DESCRIPTION:	1.2MM THK. METAL FLUSH DOOR W/ 1.2MM THK. STAINLESS STEEL 304 HAIRLINE FINISH KICK PLATE (0.30M HIGH), DOOR HANDLE ON BOTH SIDES, PRIVACY INDICATOR (VACANT / OCCUPIED) DEADBOLT LATCH AND DOOR CLOSER
LOCATION:	PWD TOILET DOOR
REQUIREMENTS:	1 SET



- Note:
- Exclude the signage
 - Include all accessories and hardwares

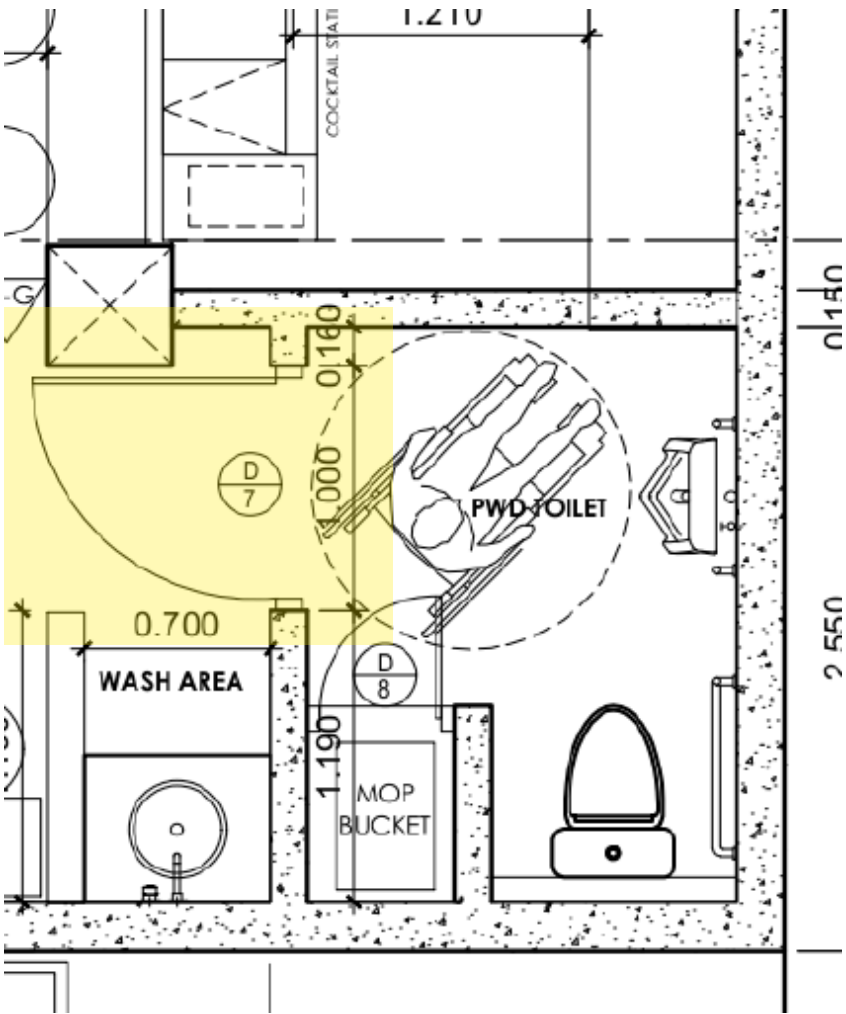

Project: 26-29


Project Location: Pasig City

5.) D-8: Single Metal Louver Door

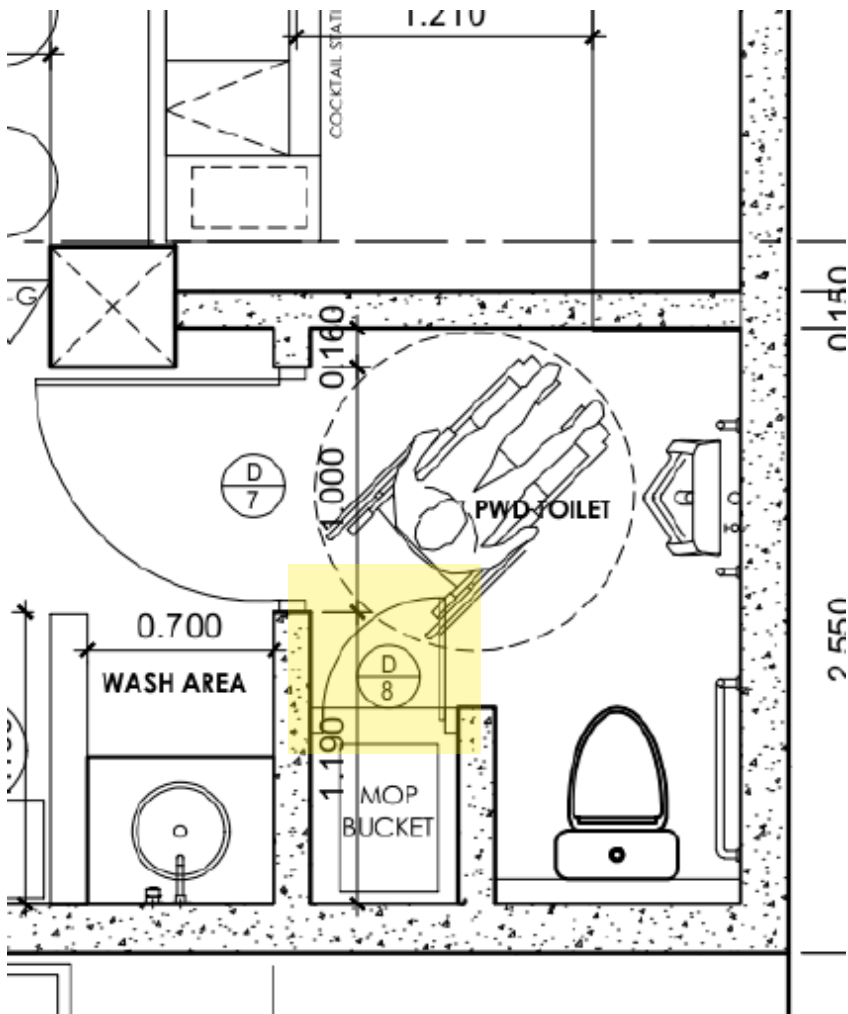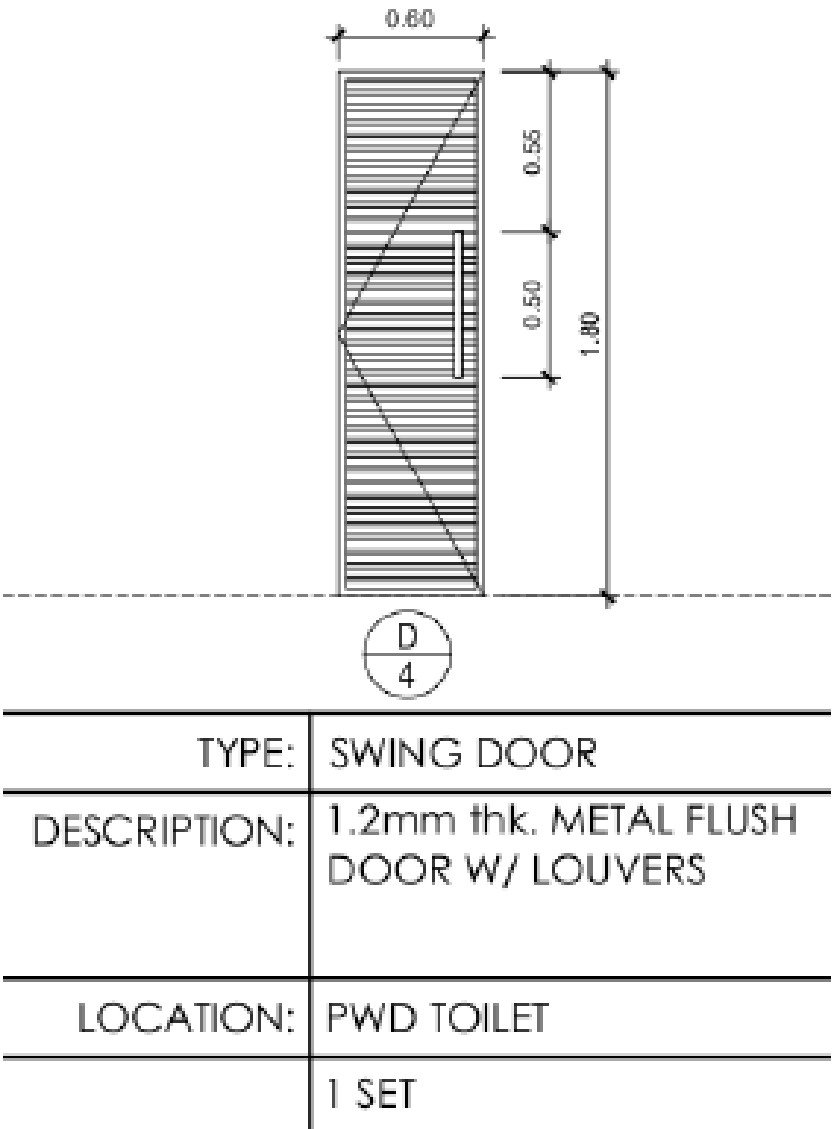


- Note:**
- Include all accessories and hardwares
 - Include Door Jamb
 - Primer Finish

6.) D-9: Double Metal Louver Door

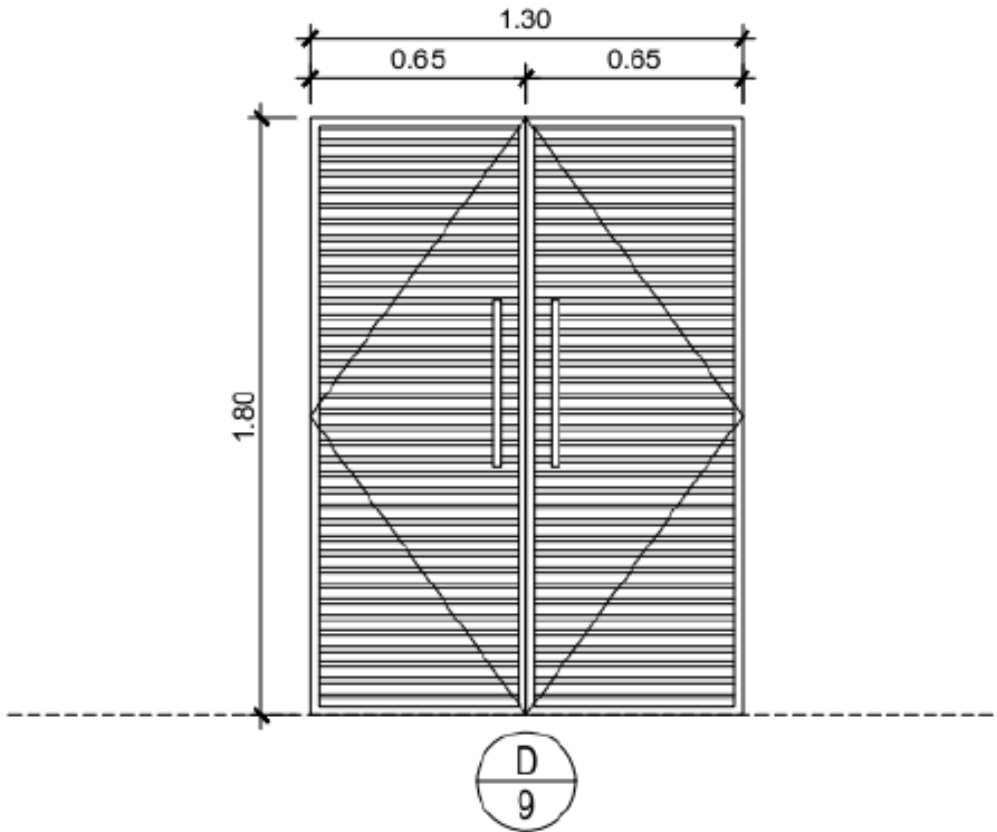


TYPE:	SWING DOOR
DESCRIPTION:	1.2mm thk. METAL FLUSH DOOR W/ LOUVERS
LOCATION:	GAS STORAGE
	1 SET

- Note:**
- Include all accessories and hardwares
 - Include Door Jamb
 - Primer Finish

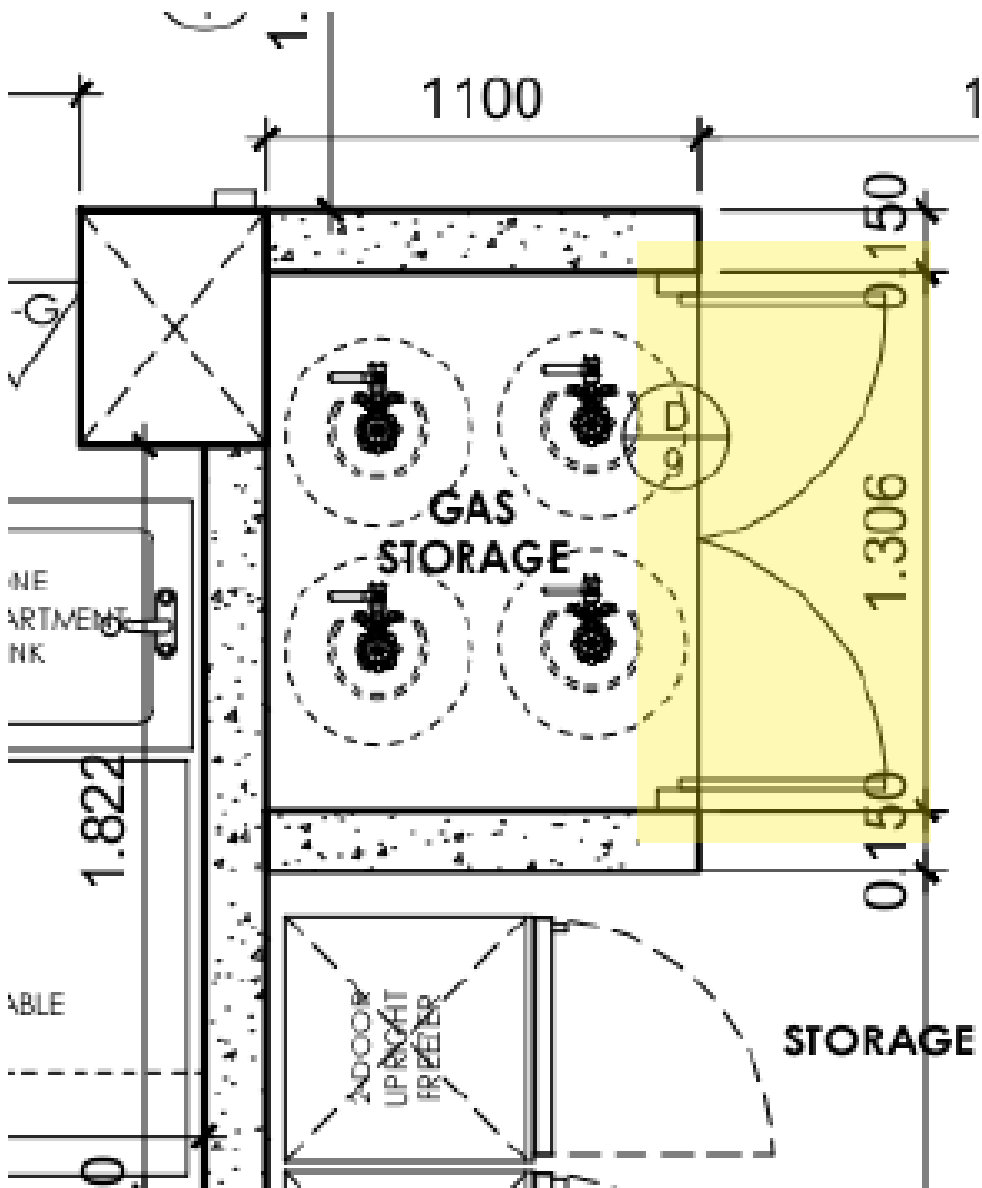


7.) W-5: Dispatch Window

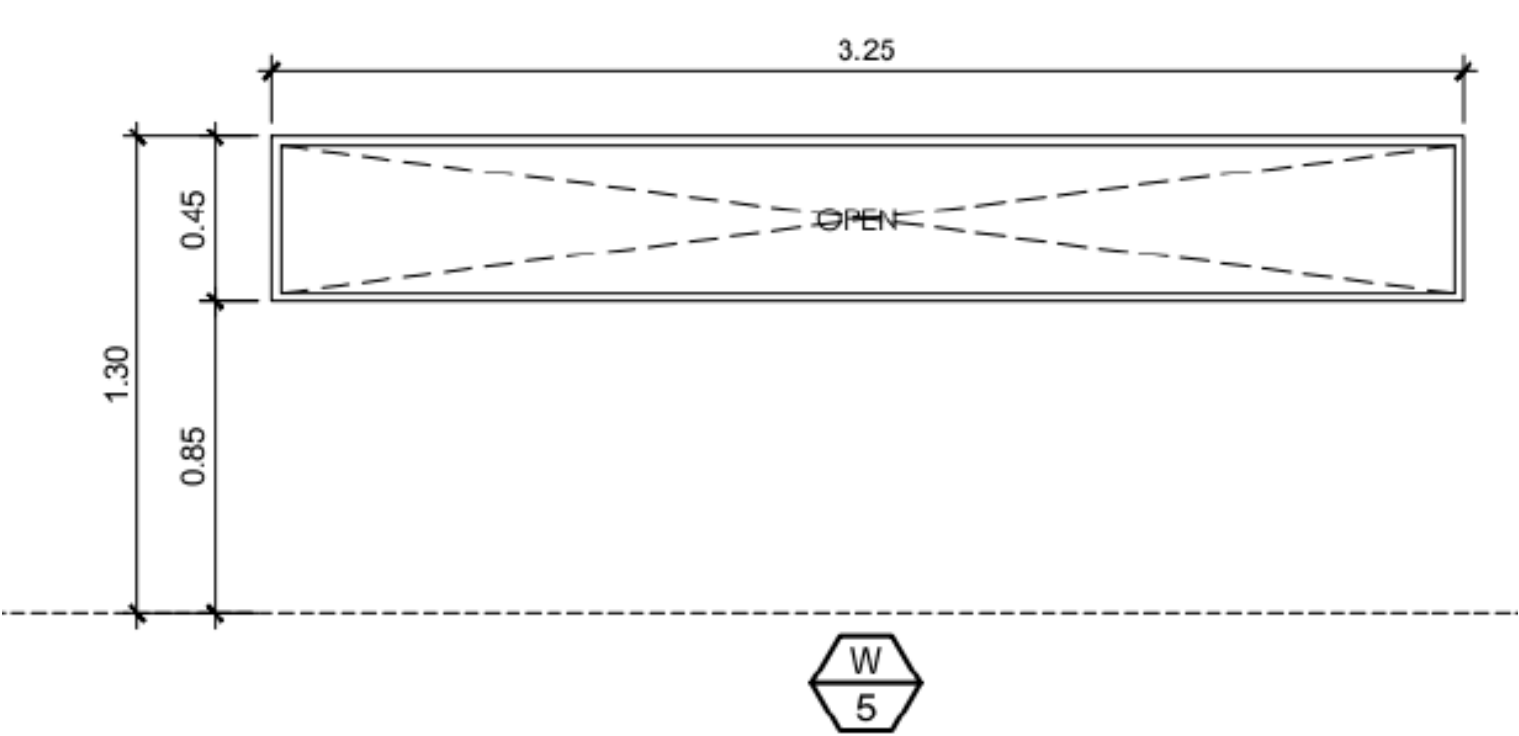


TYPE:	OPEN WINDOW
DESCRIPTION:	STAINLESS STEEL DISPATCH WINDOW
LOCATION:	DISPATCH AREA
REQUIREMENTS:	1 SET

Option 1: 25mm x 150mm Stainless Tubular

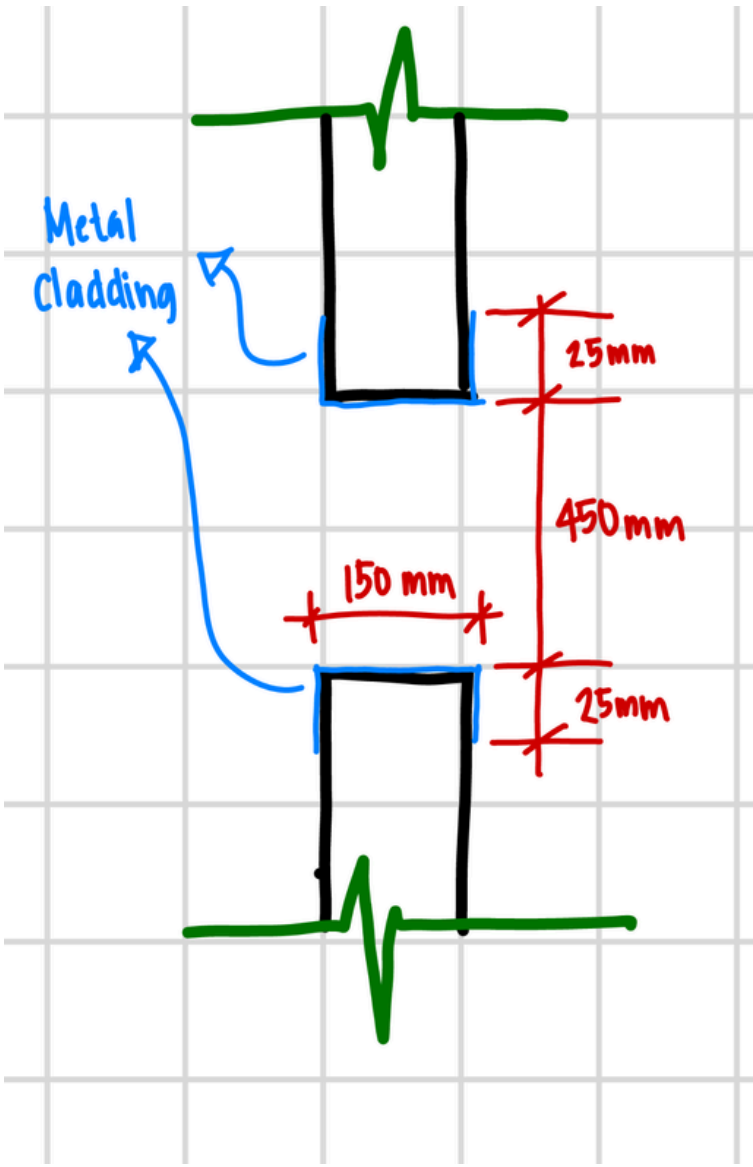


Option 2: 1.2mm thk Stainless Steel Cladding

8.) W-6: Bussing Window

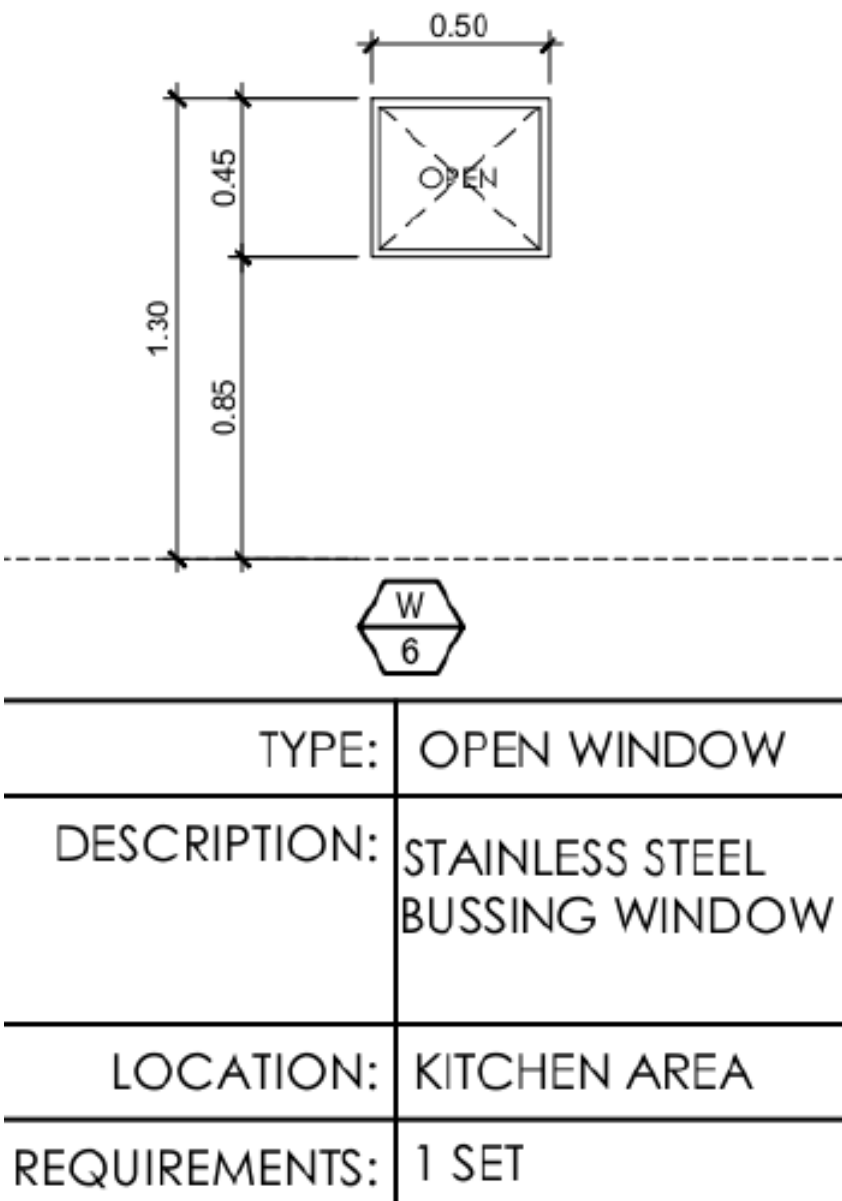

Option 1: 25mm x 150mm Stainless Tubular

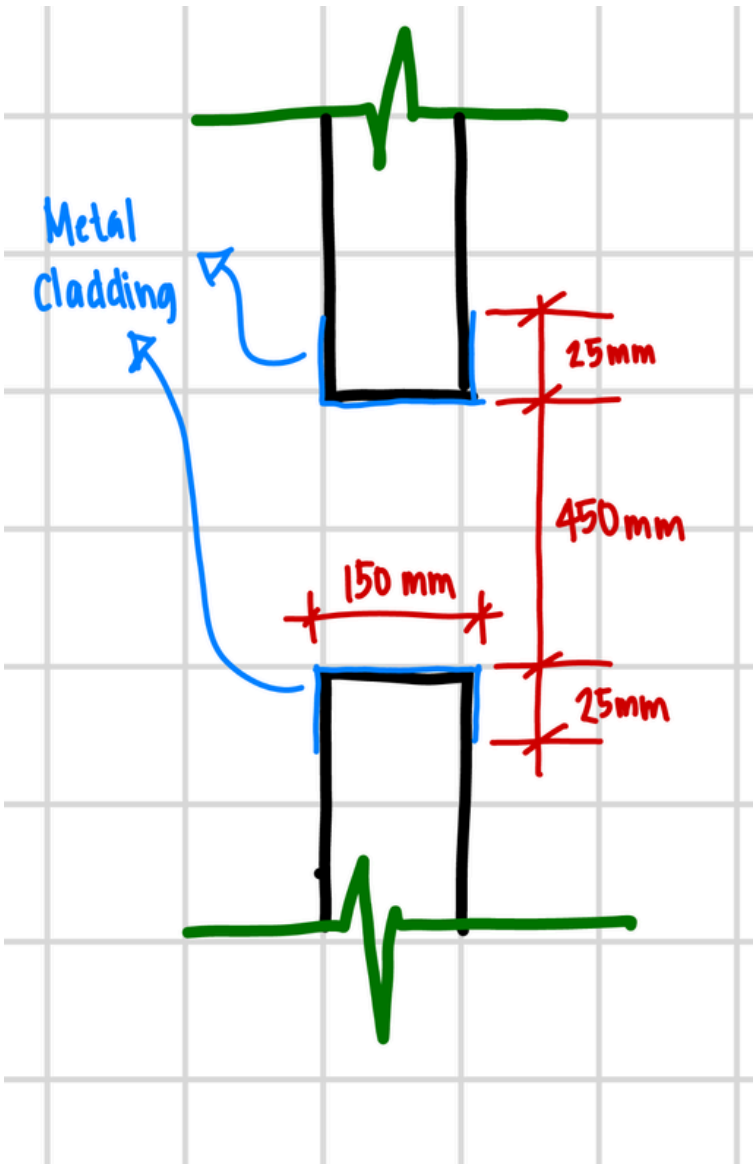

Option 2: 1.2mm thk Stainless Steel Cladding